



URBAN FORESTRY CENTER

Lucia Tian
INTERMEDIATE ARCHITECTURAL DESIGN
Brown University


URBAN FORESTRY CENTER


This is an Urban Forestry and Environmental Education Center that helps trees to be planted in the city adjust to the Providence environment while educating the public about the environment. Starting from site analysis to conceptual designs to plans and renderings, this presentation shows my thought process in designing a public space that draws in pedestrians from downtown Providence and riverside greenspaces to a community courtyard space that leads into the building program.








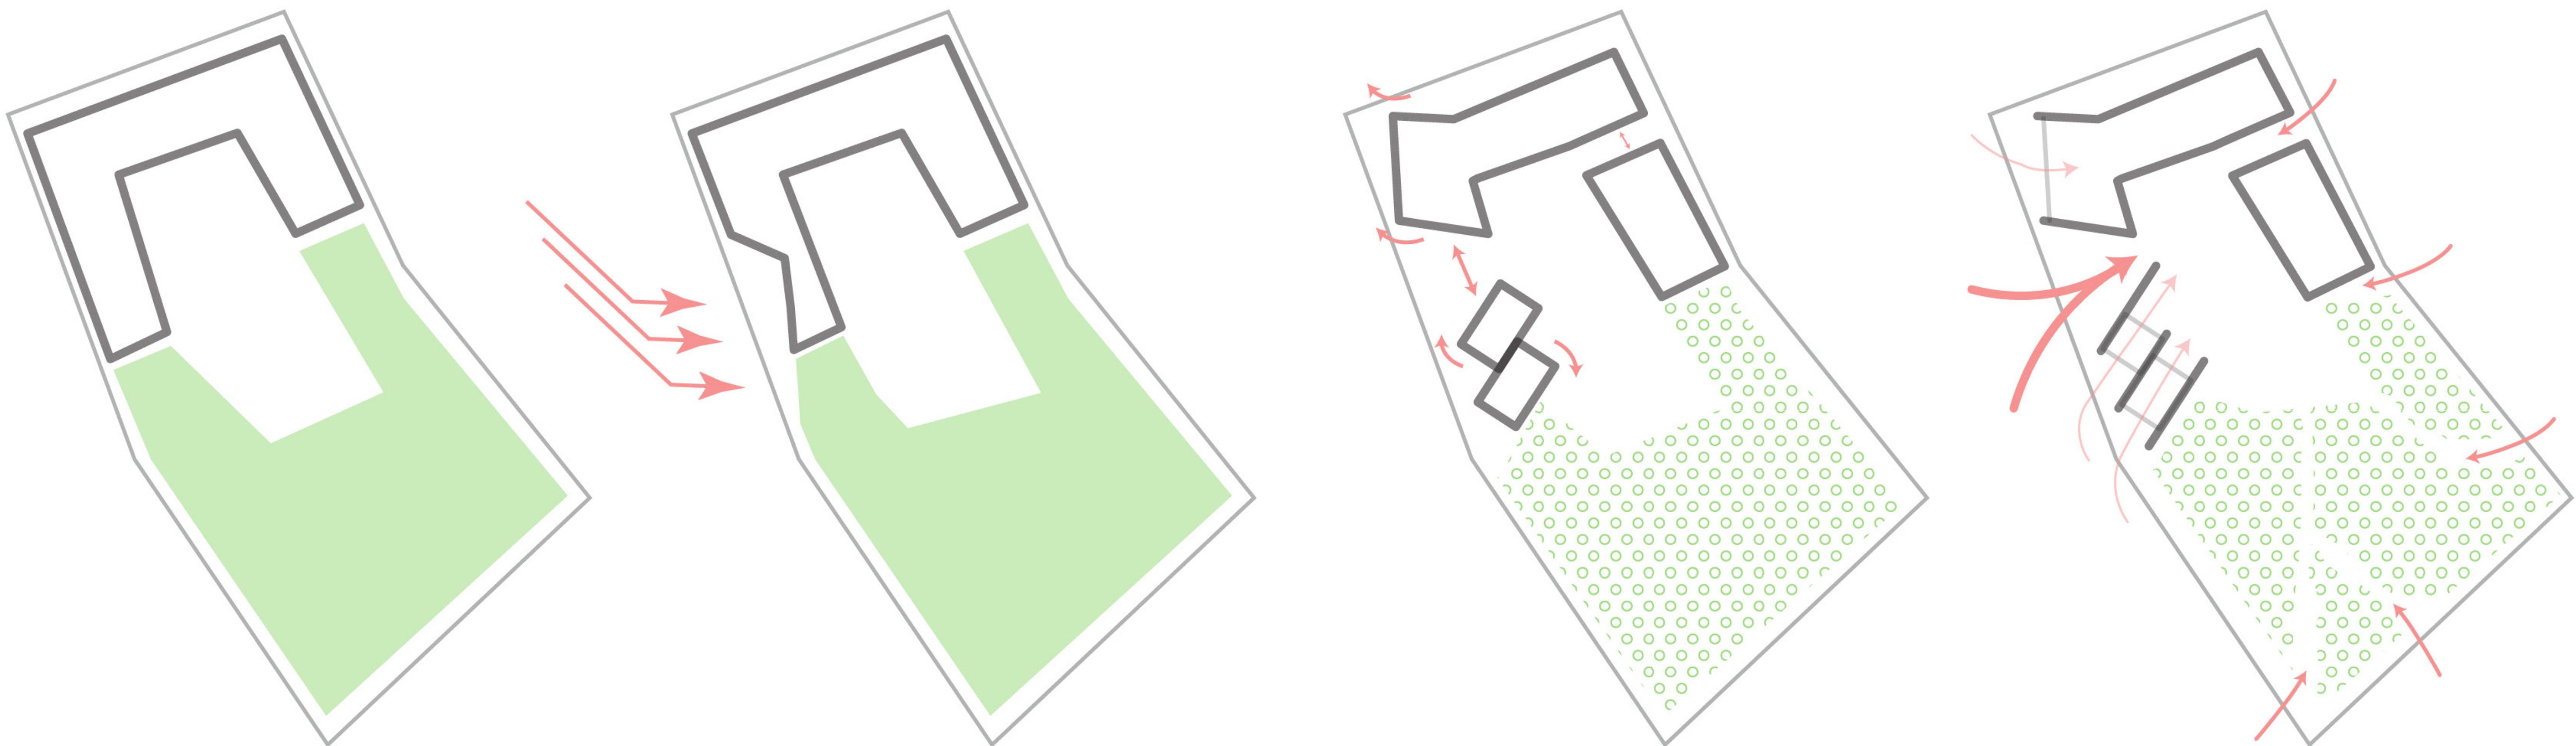

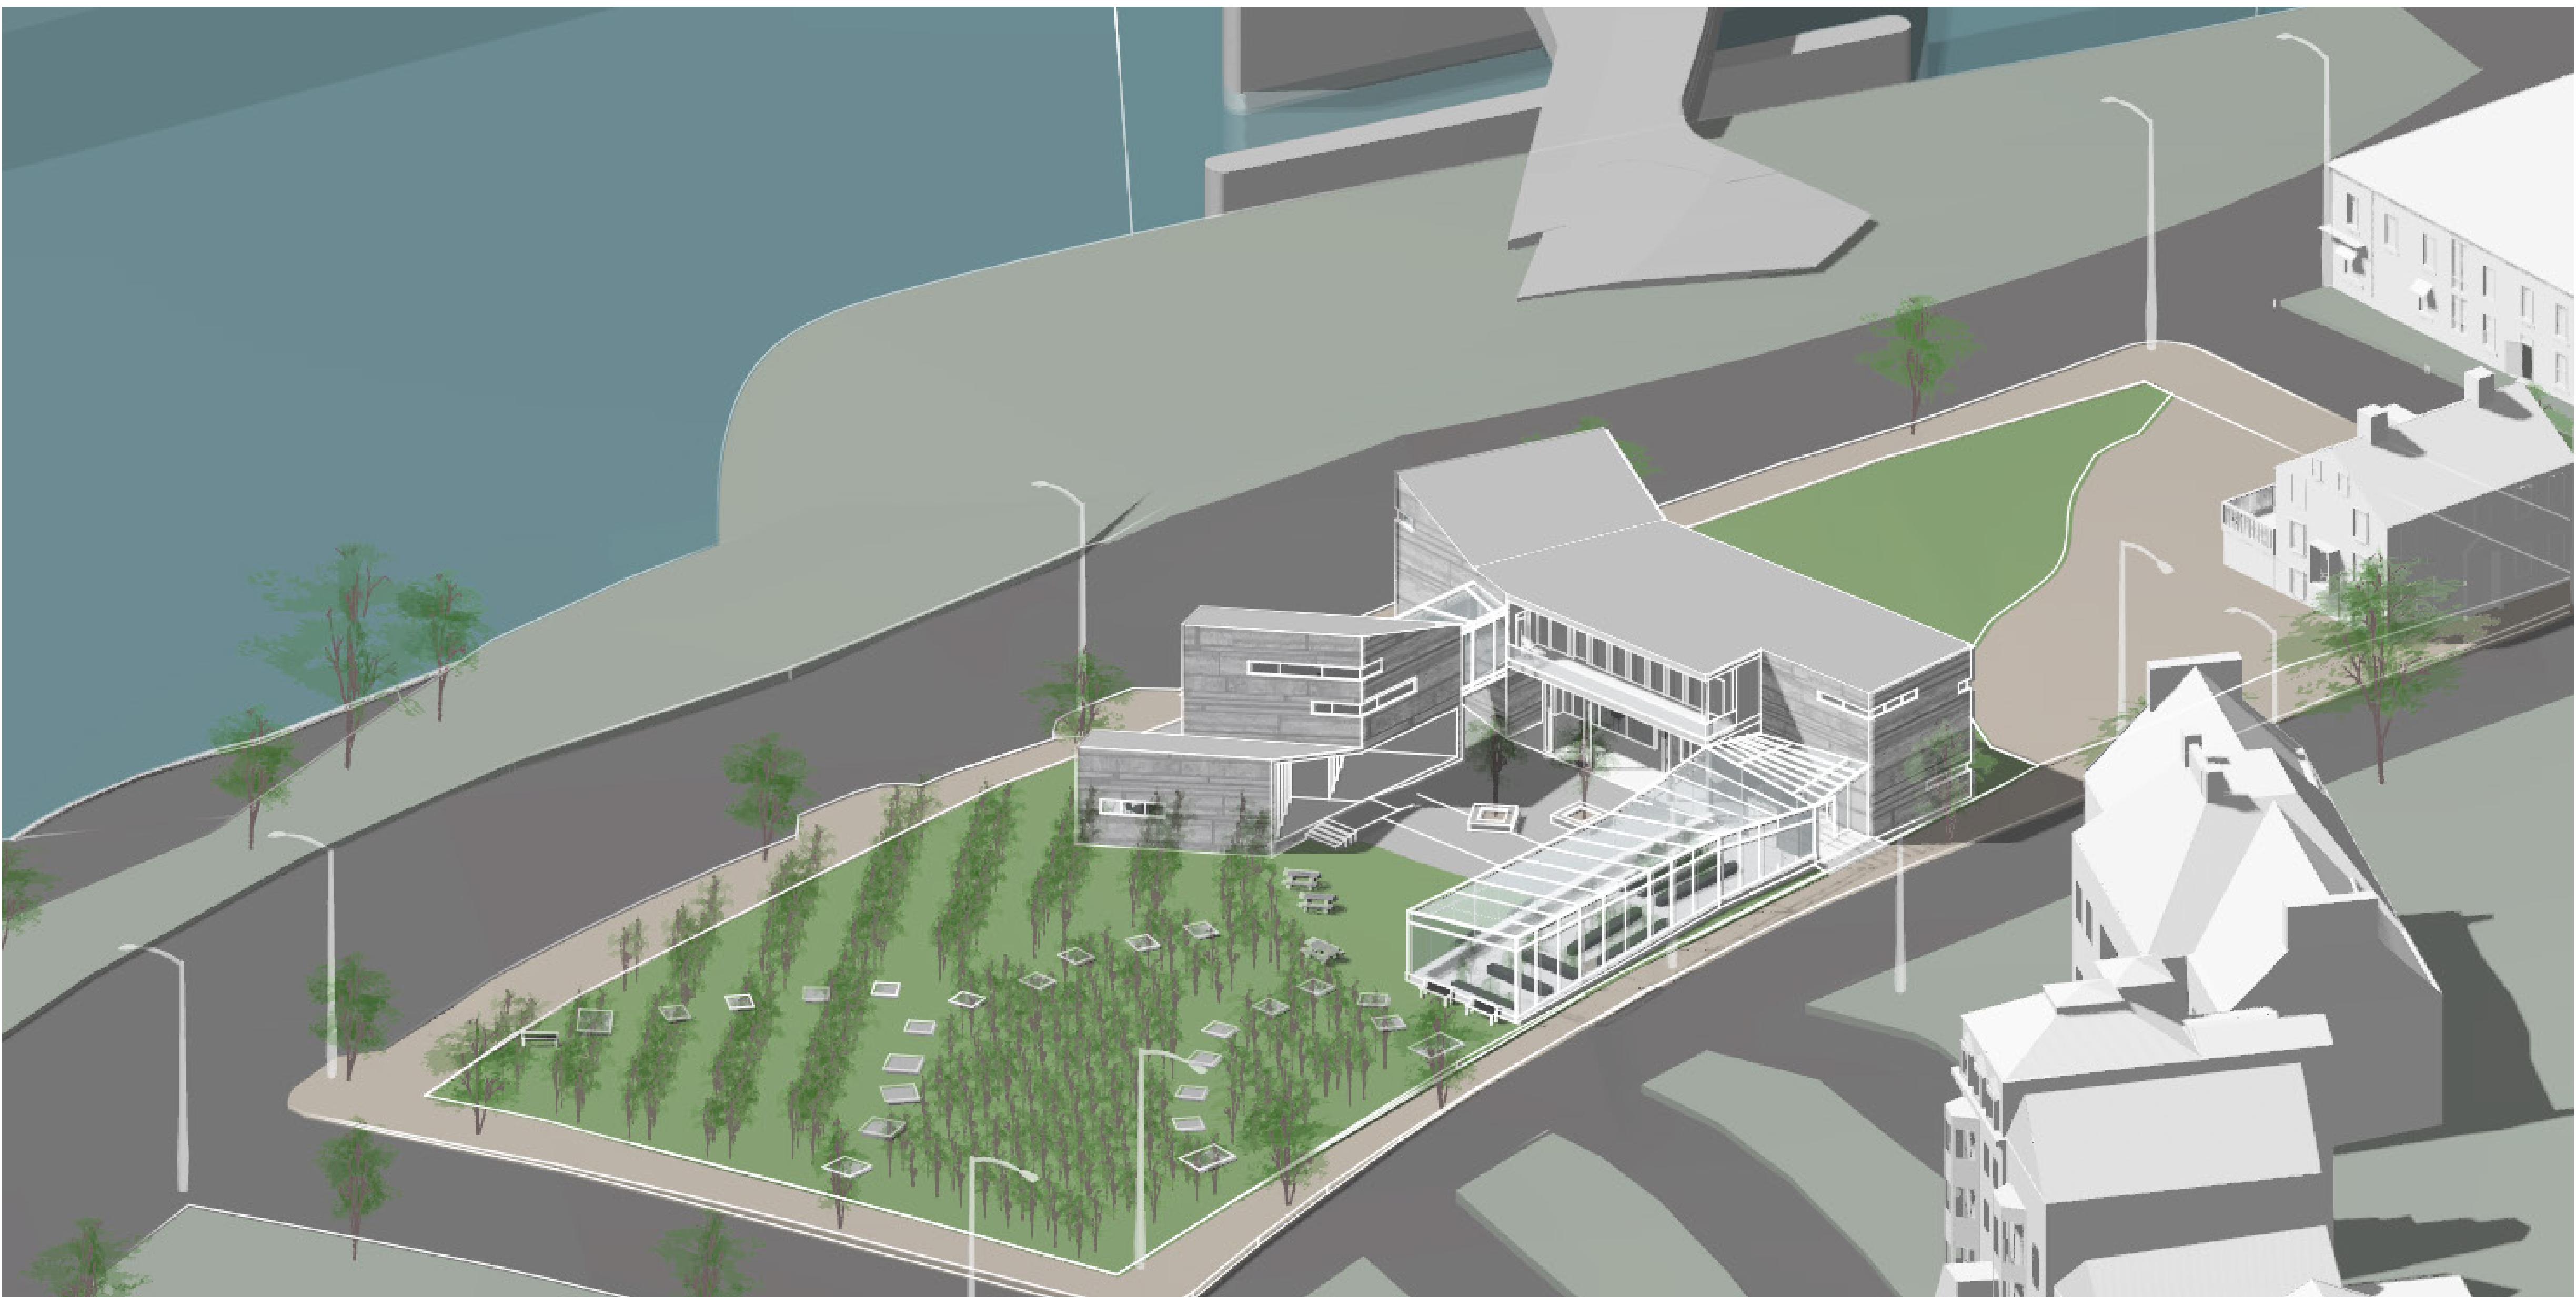


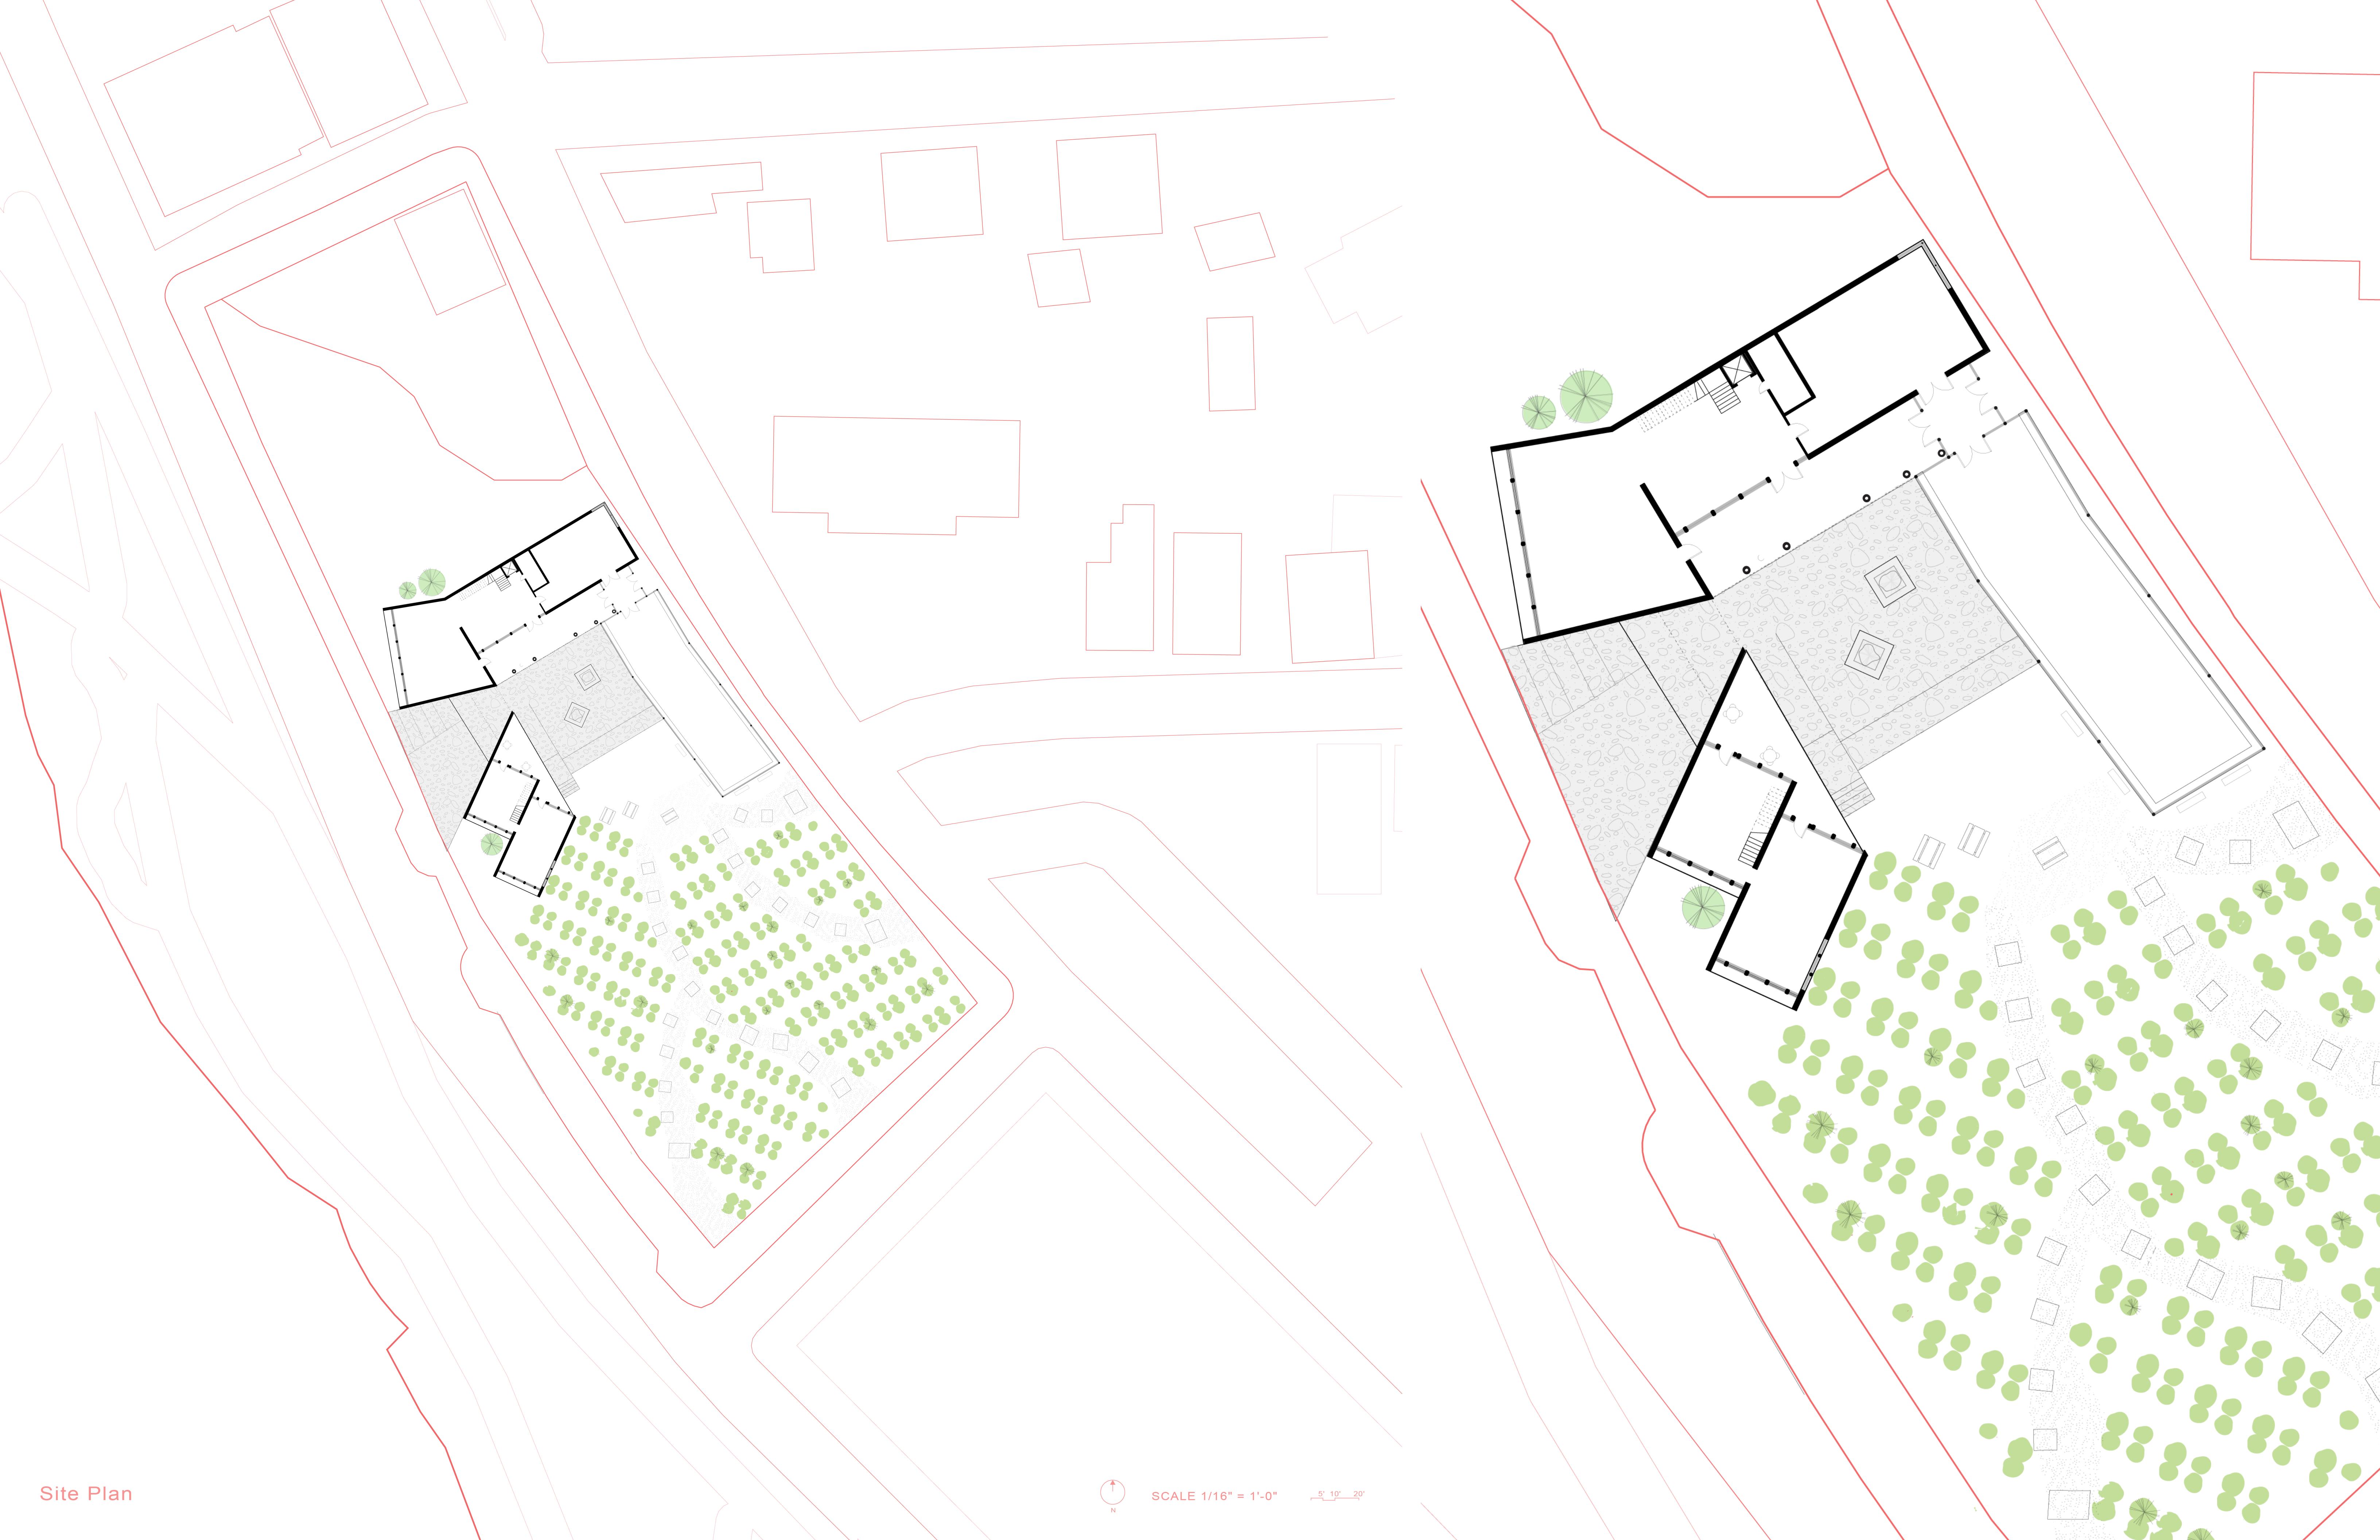

Site Plan

N
SCALE 1/16" = 1'-0"
5' 10' 20'



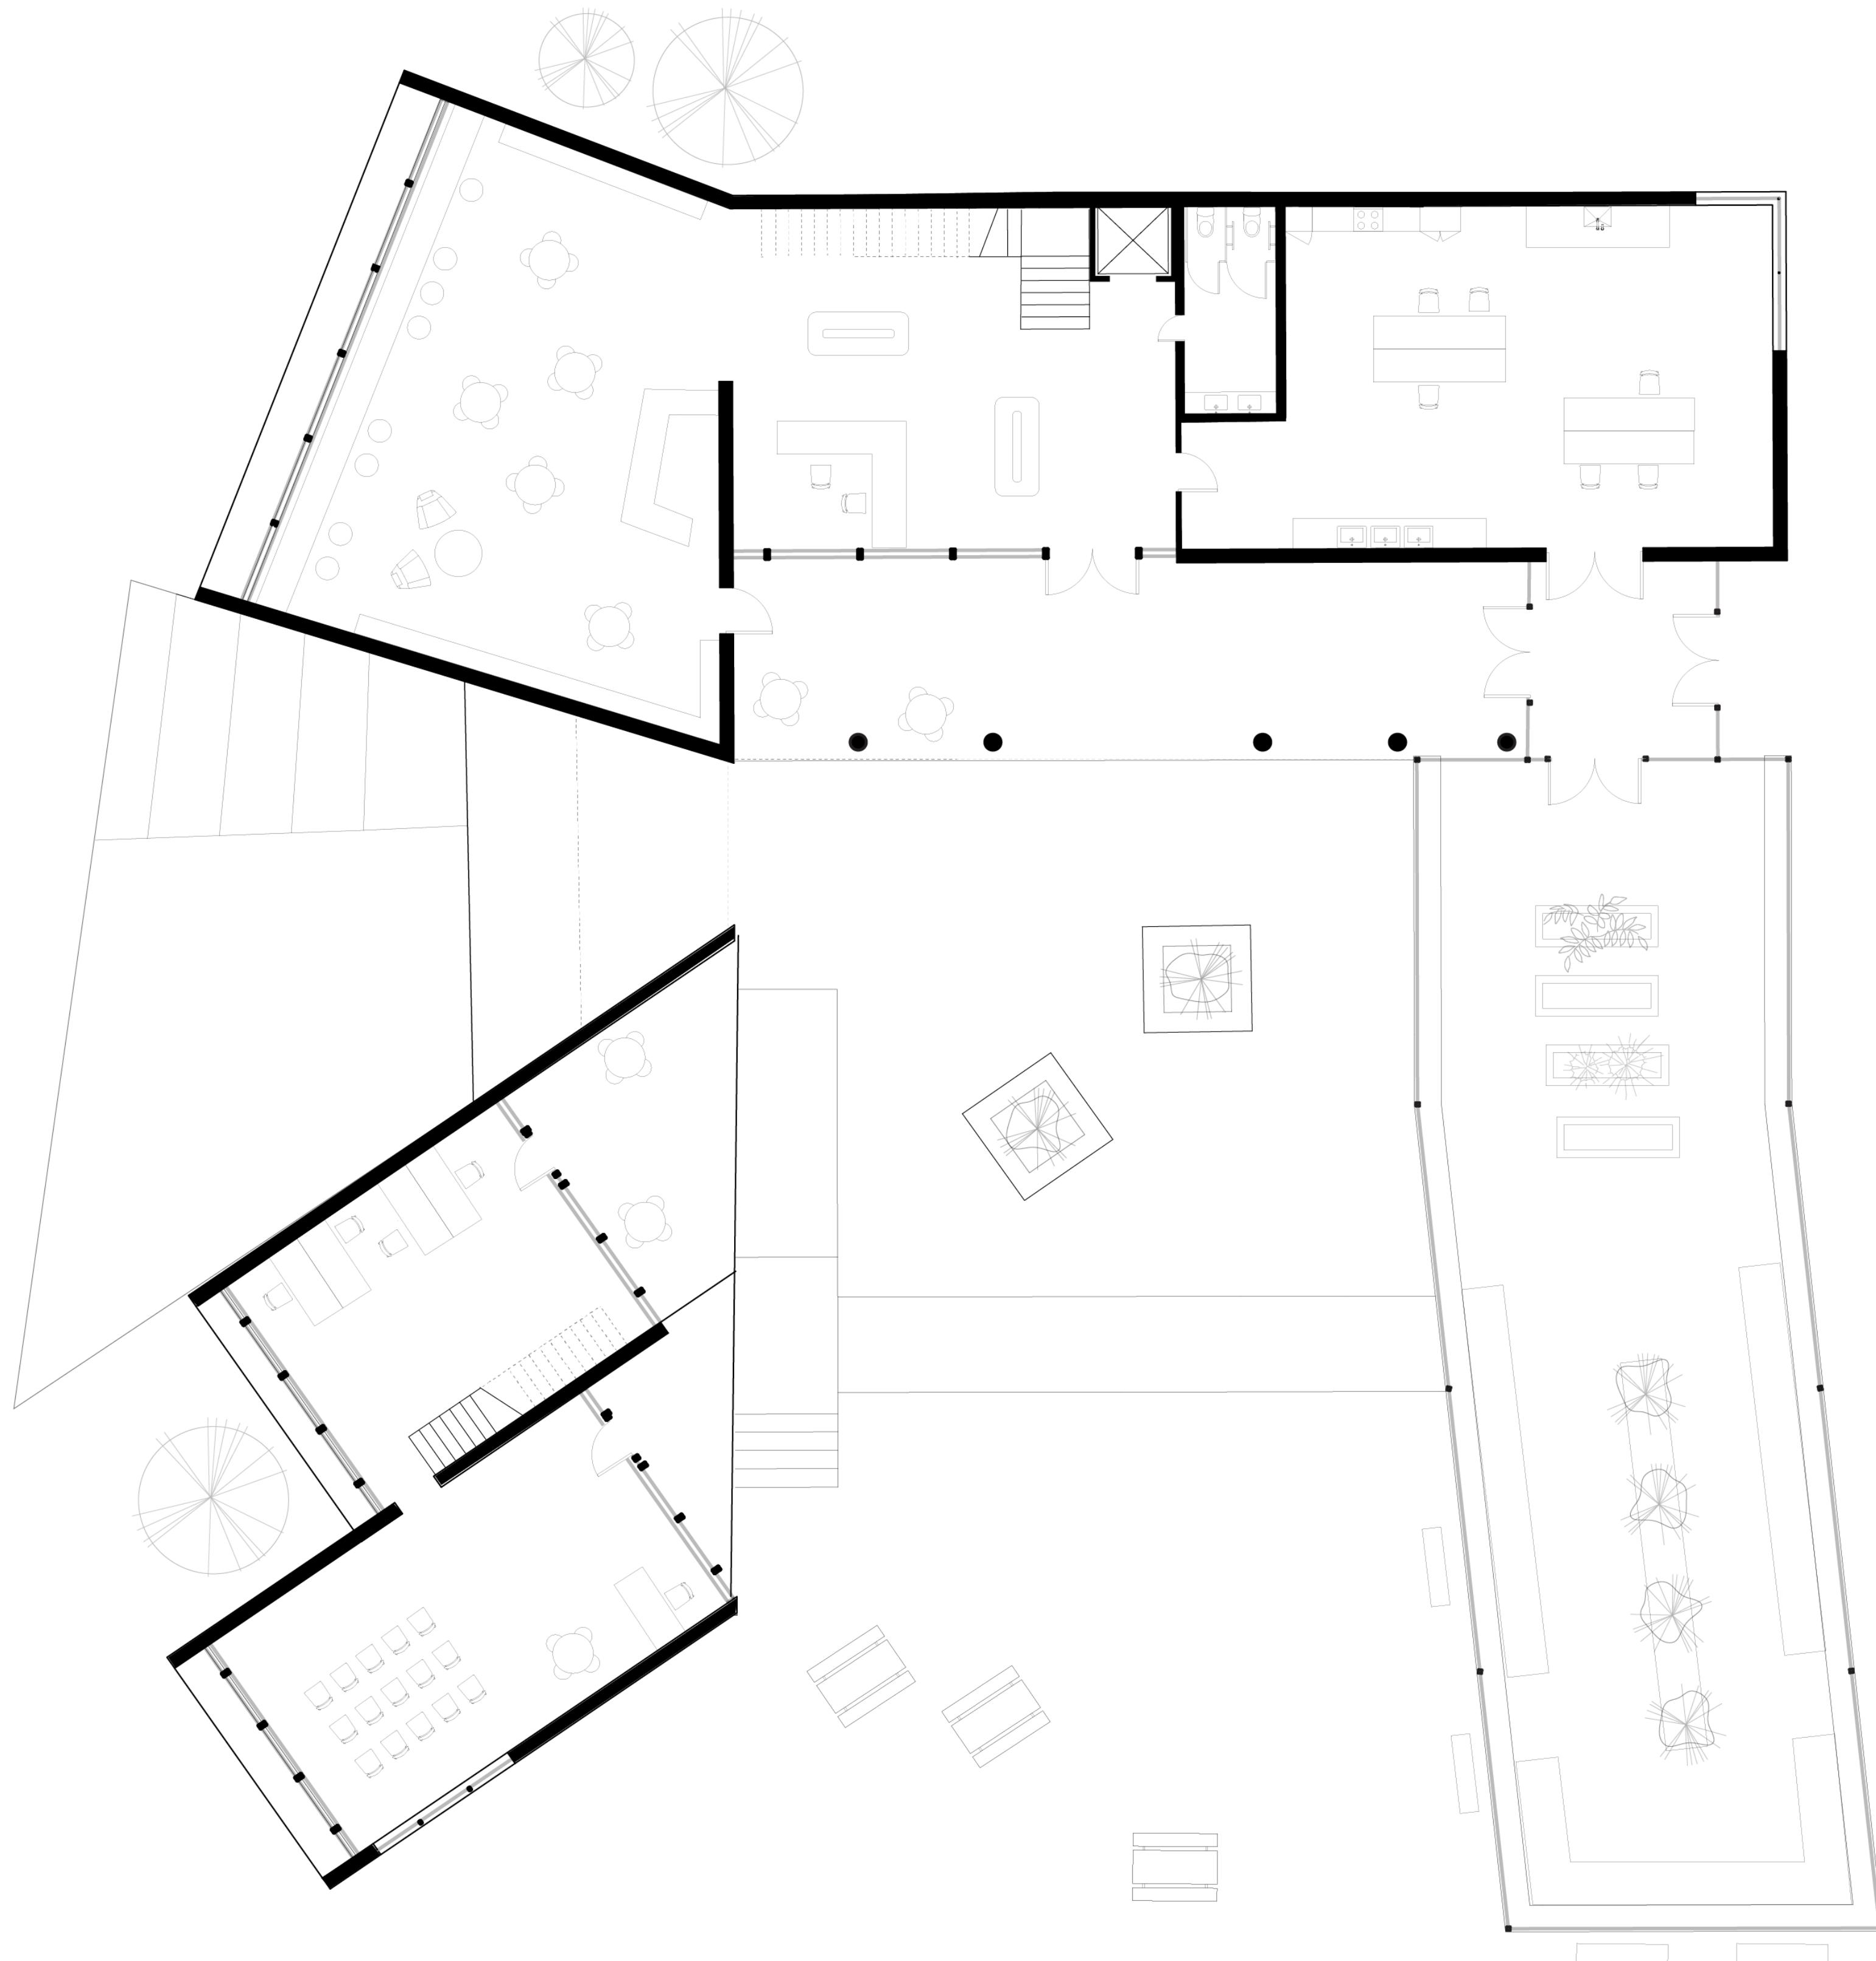


Floor 1




SCALE 1/8" = 1'-0"

5' 10' 20'

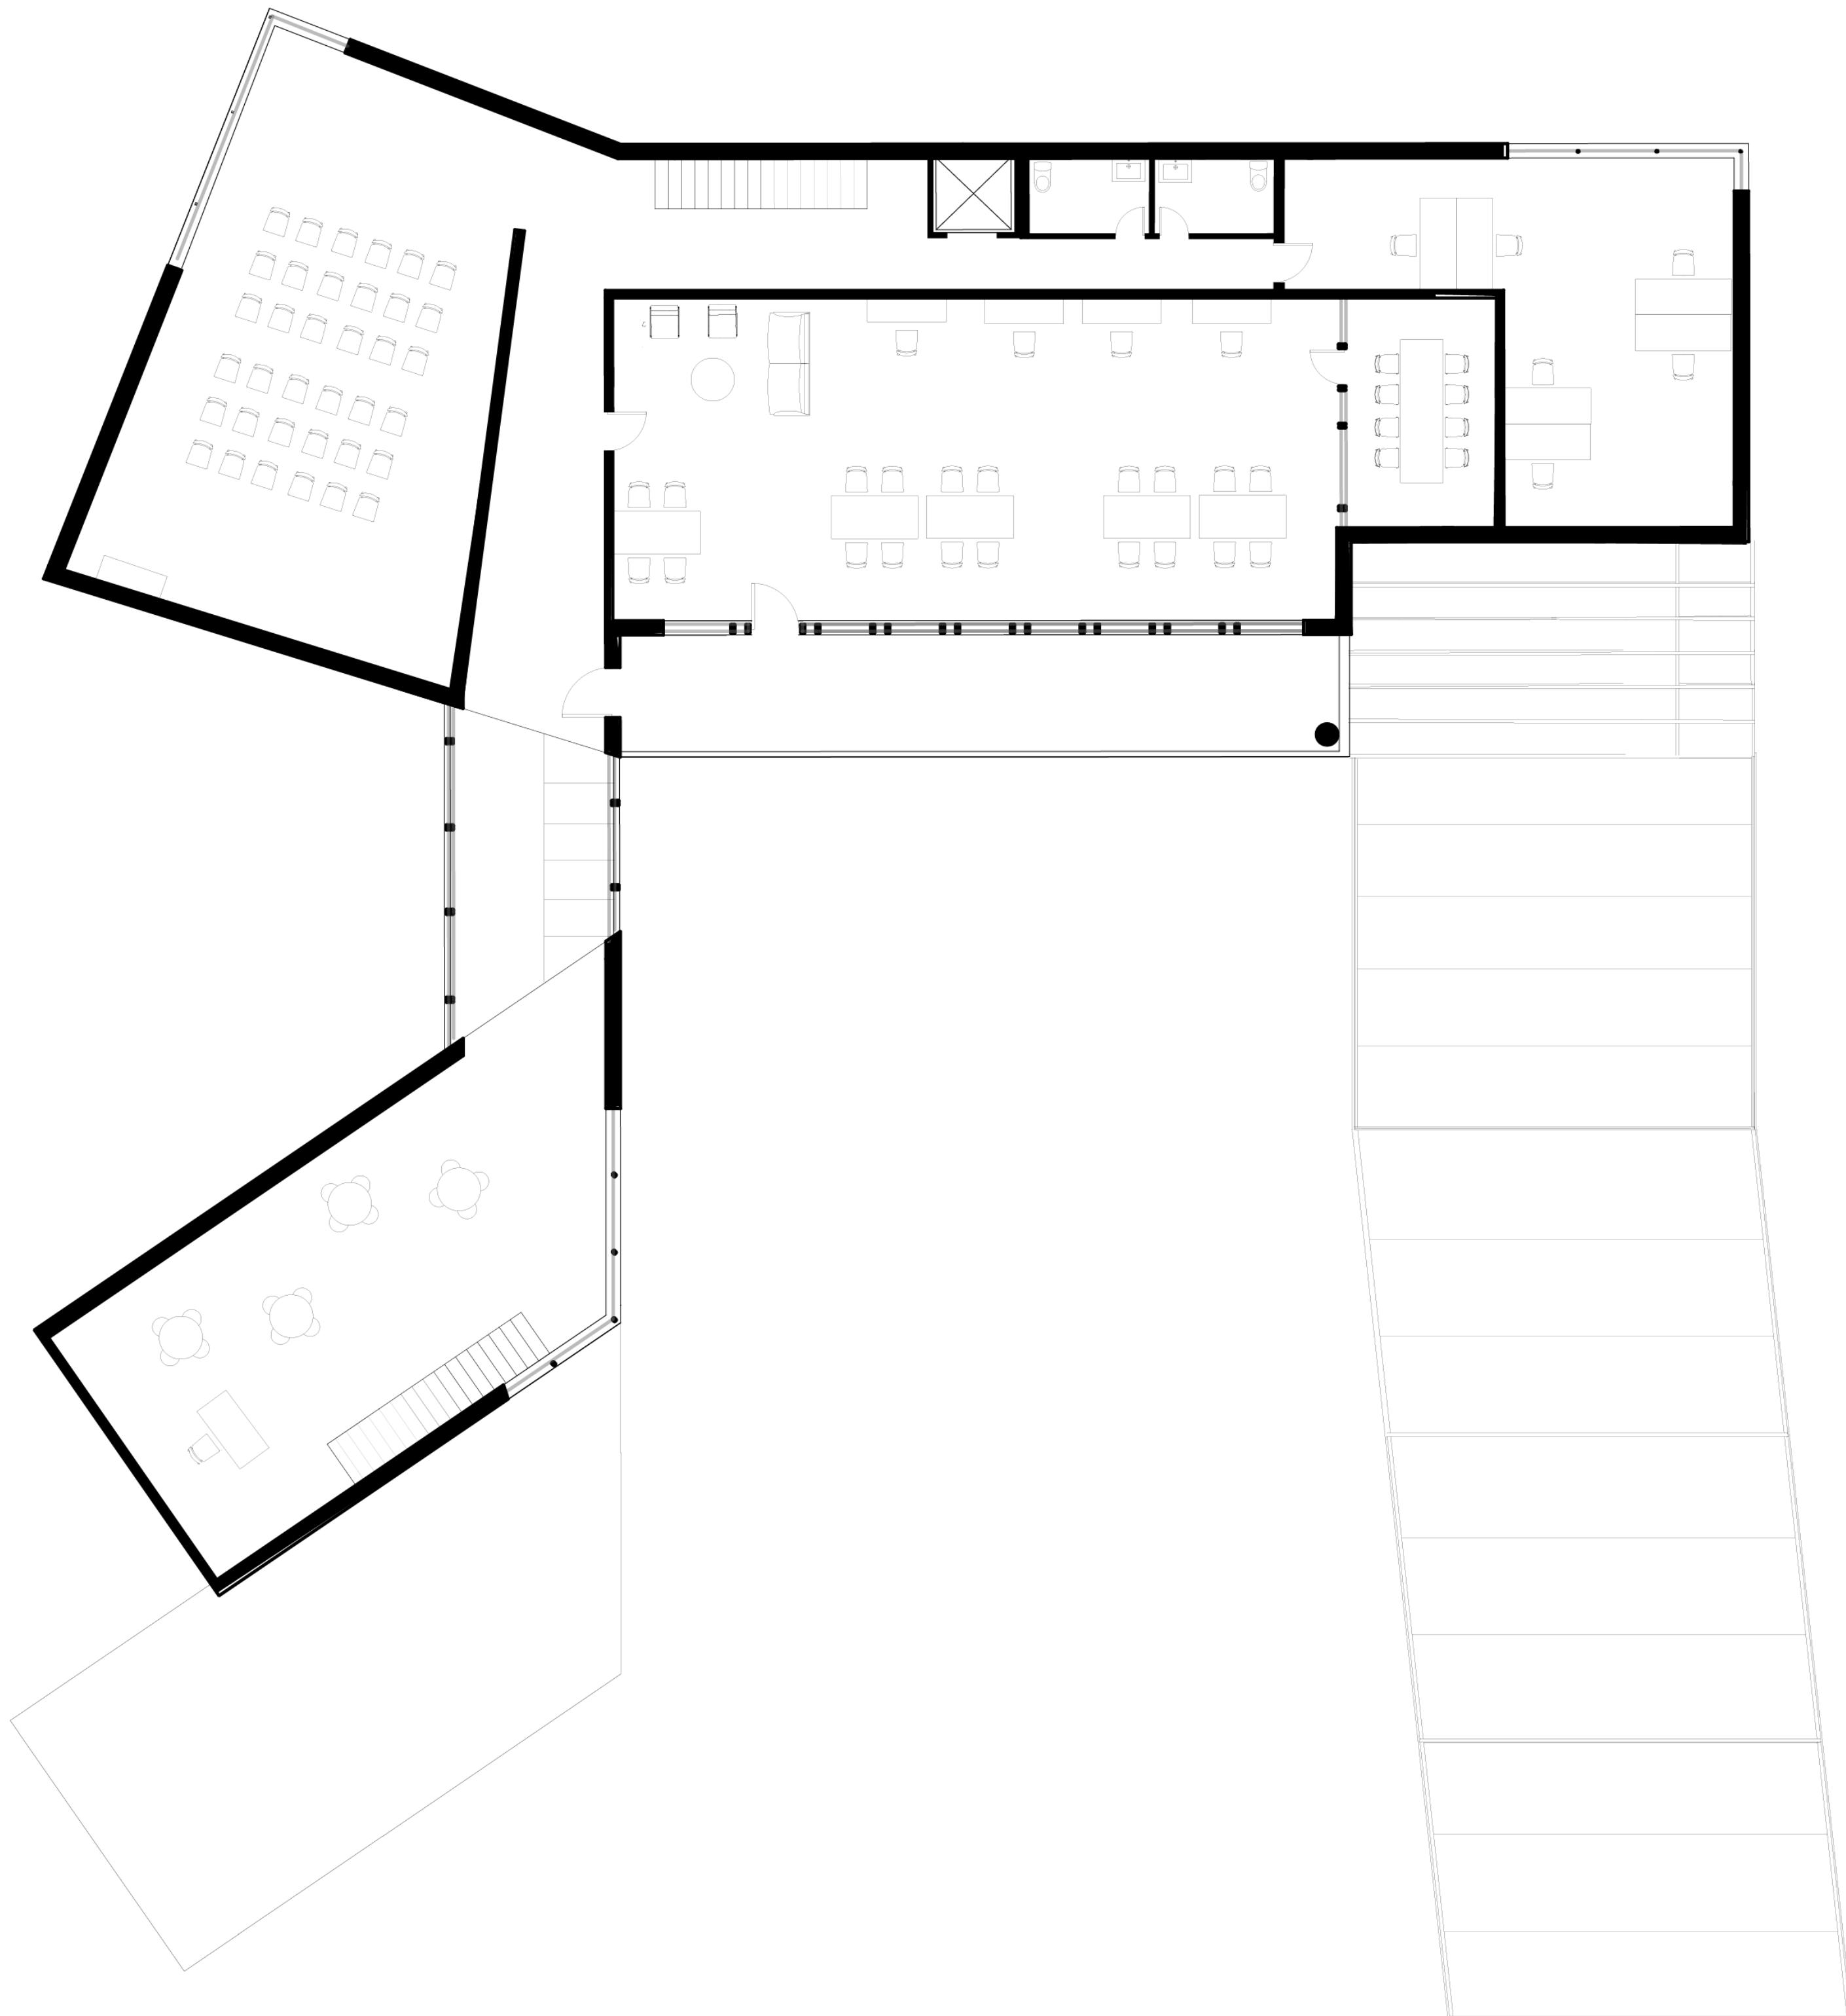

Floor 2

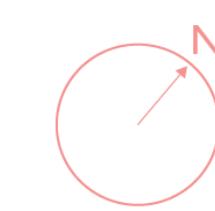


SCALE 1/8" = 1'-0"


5' 10' 20'








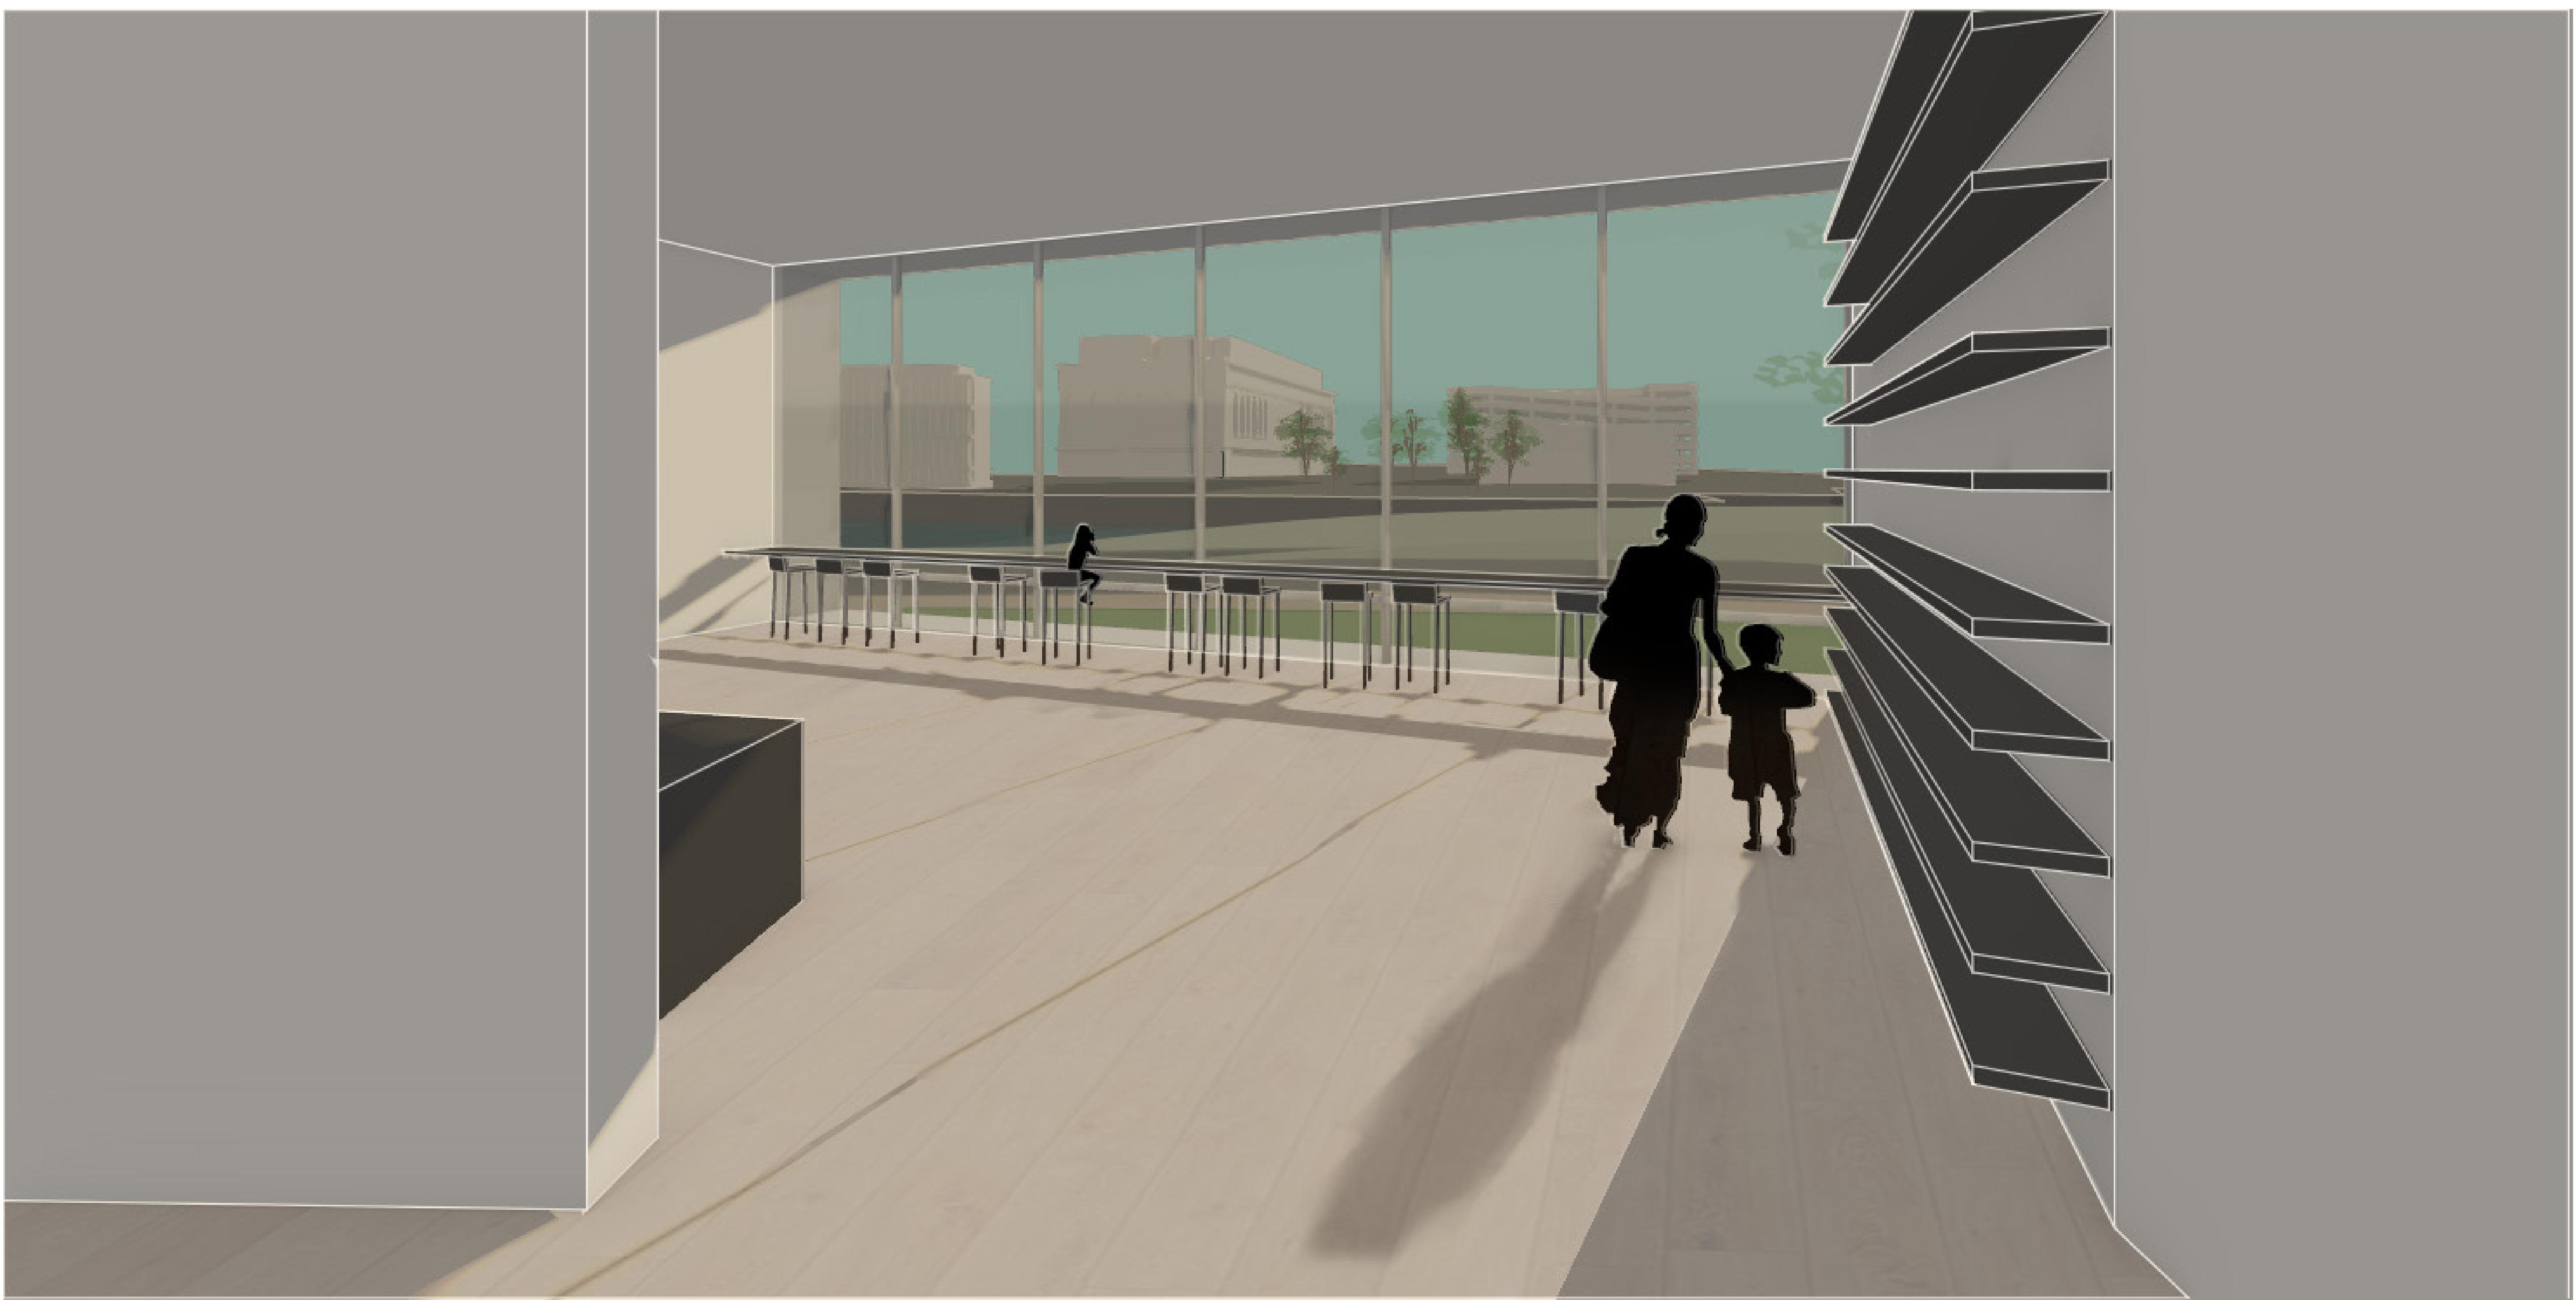


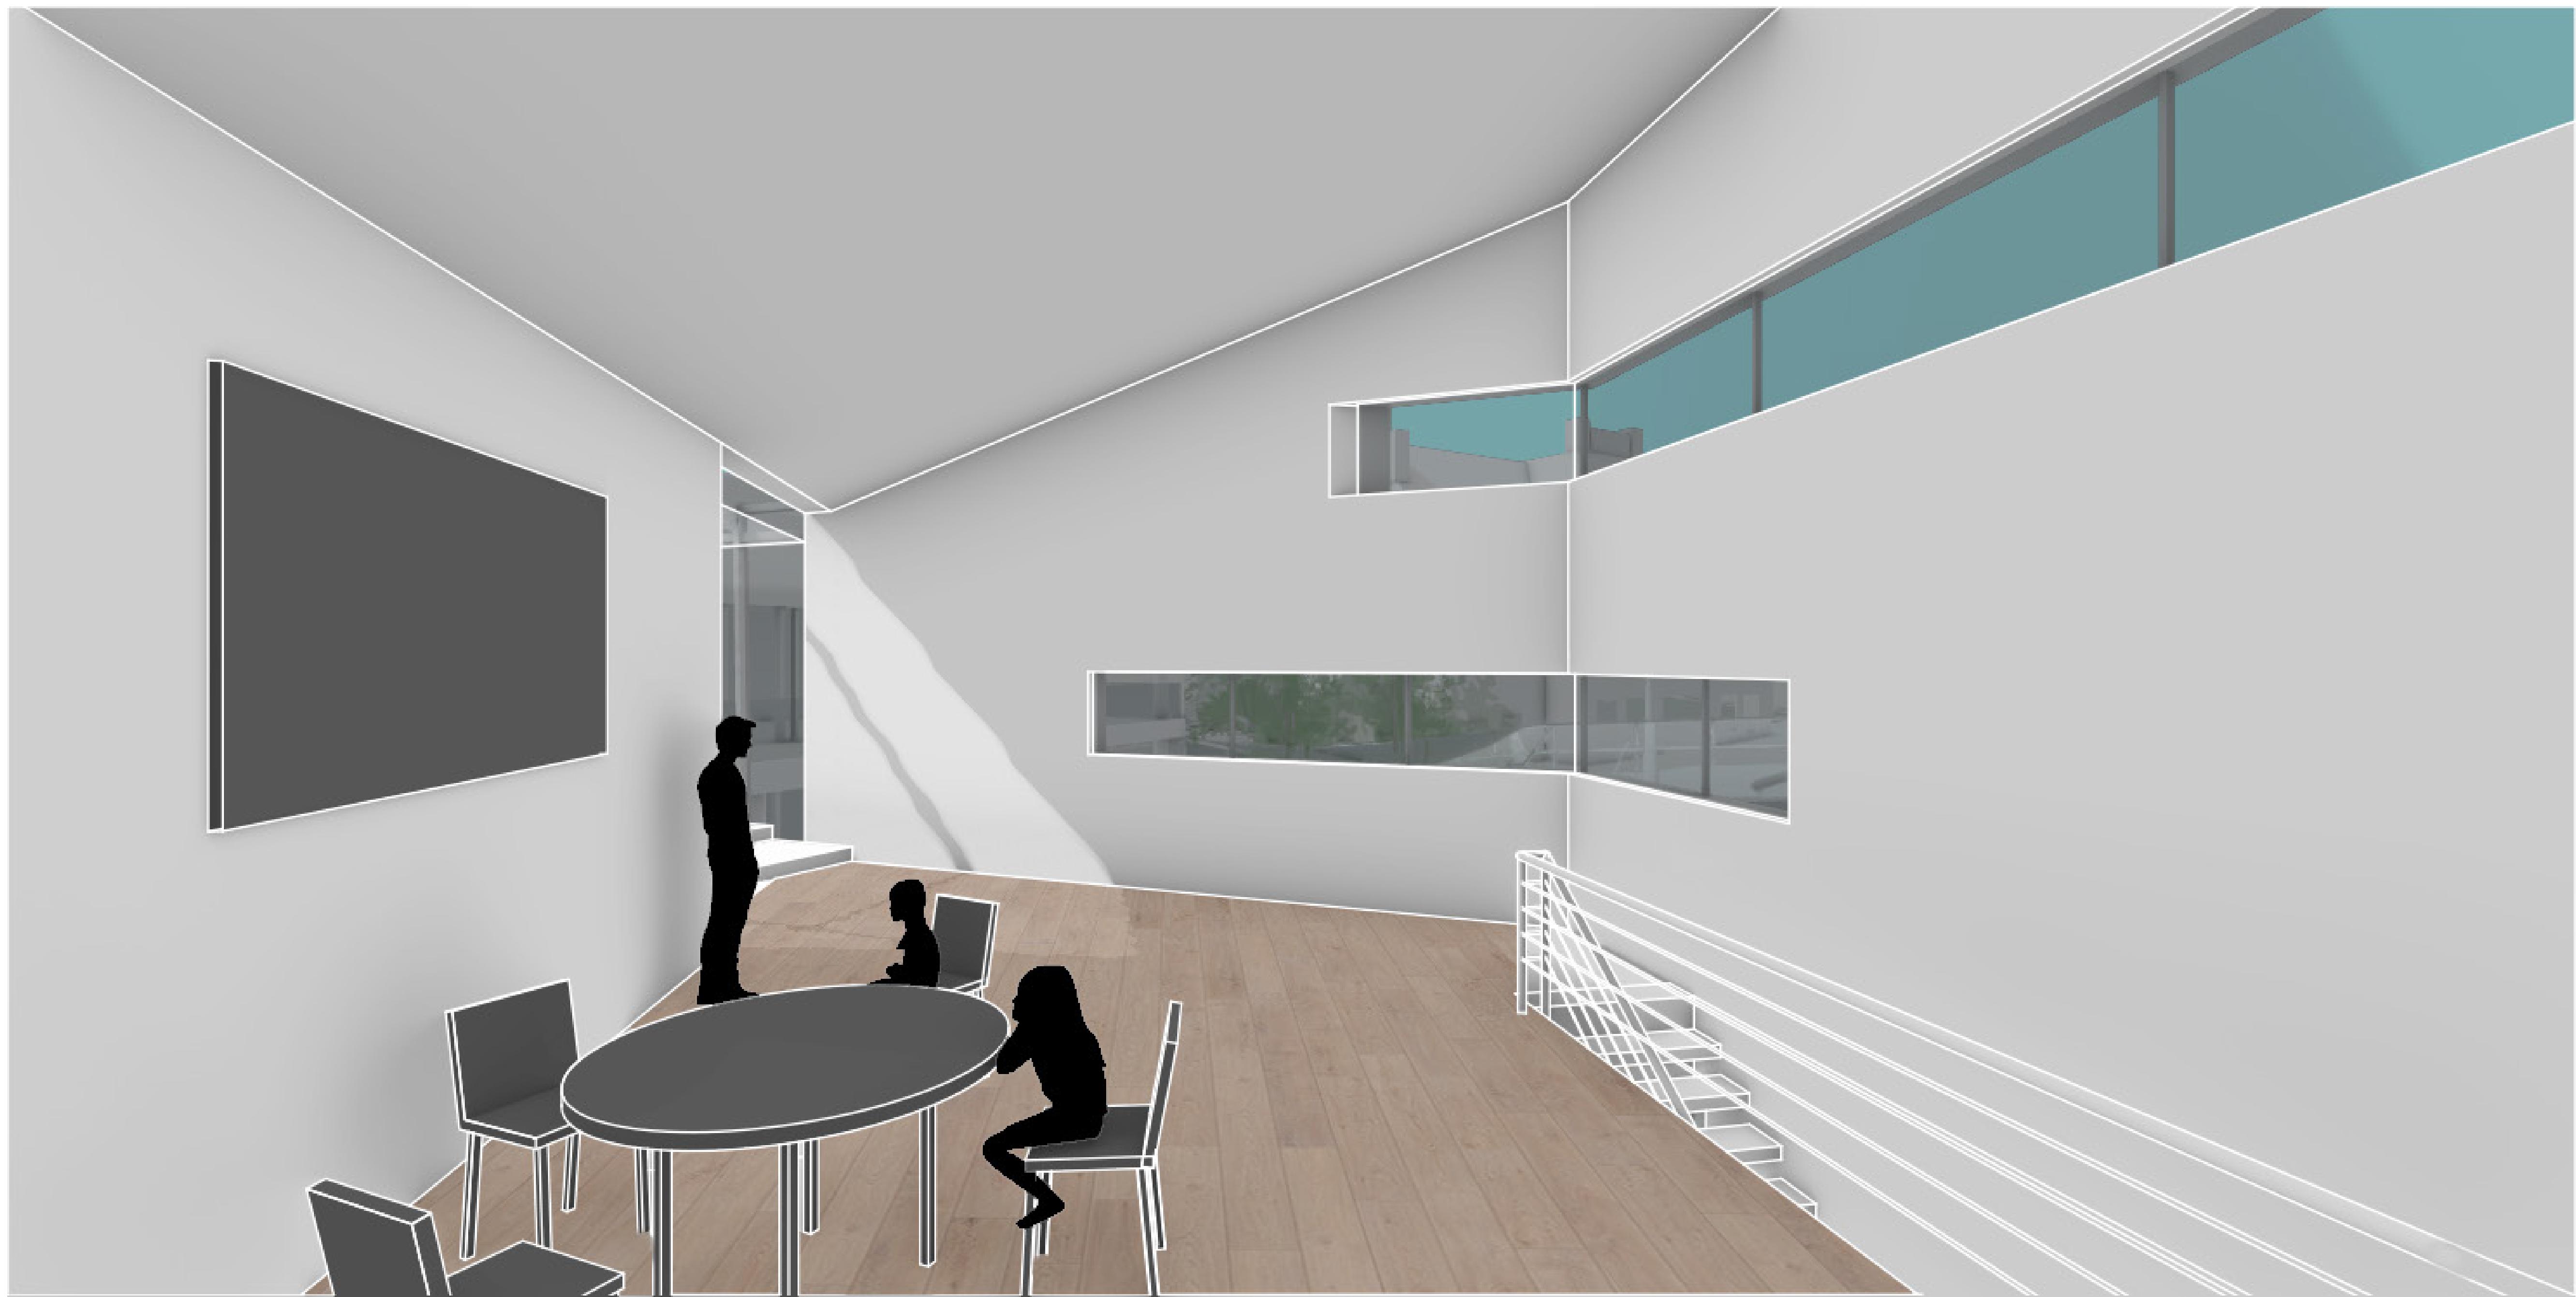


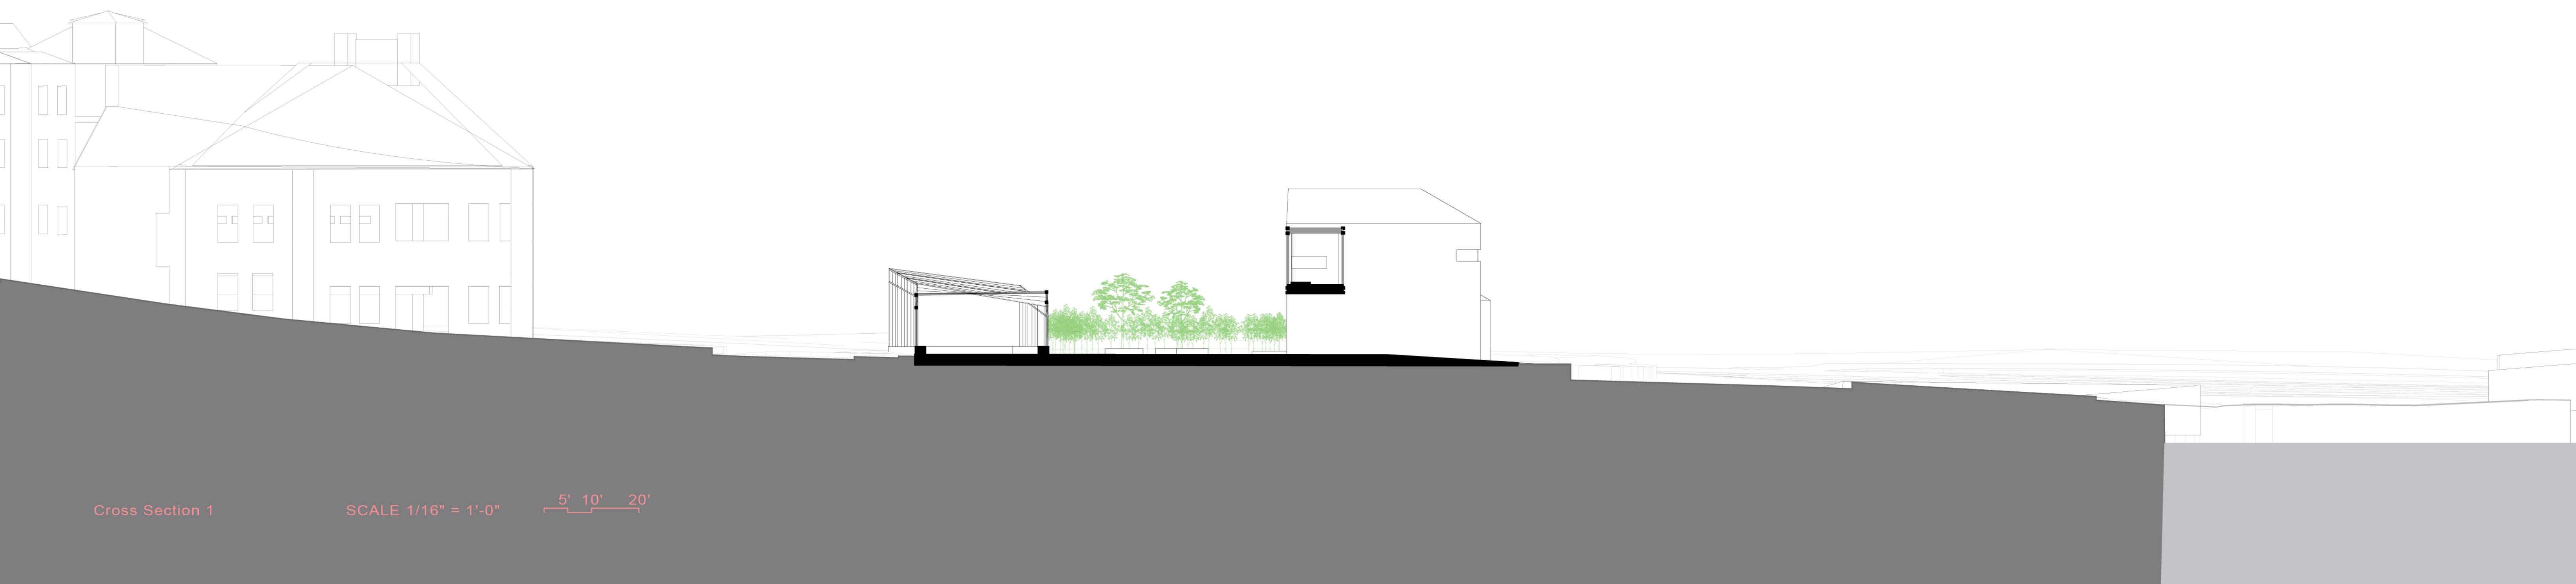

Cross Section 1





SCALE 1/16" = 1'-0"
5' 10" 20"

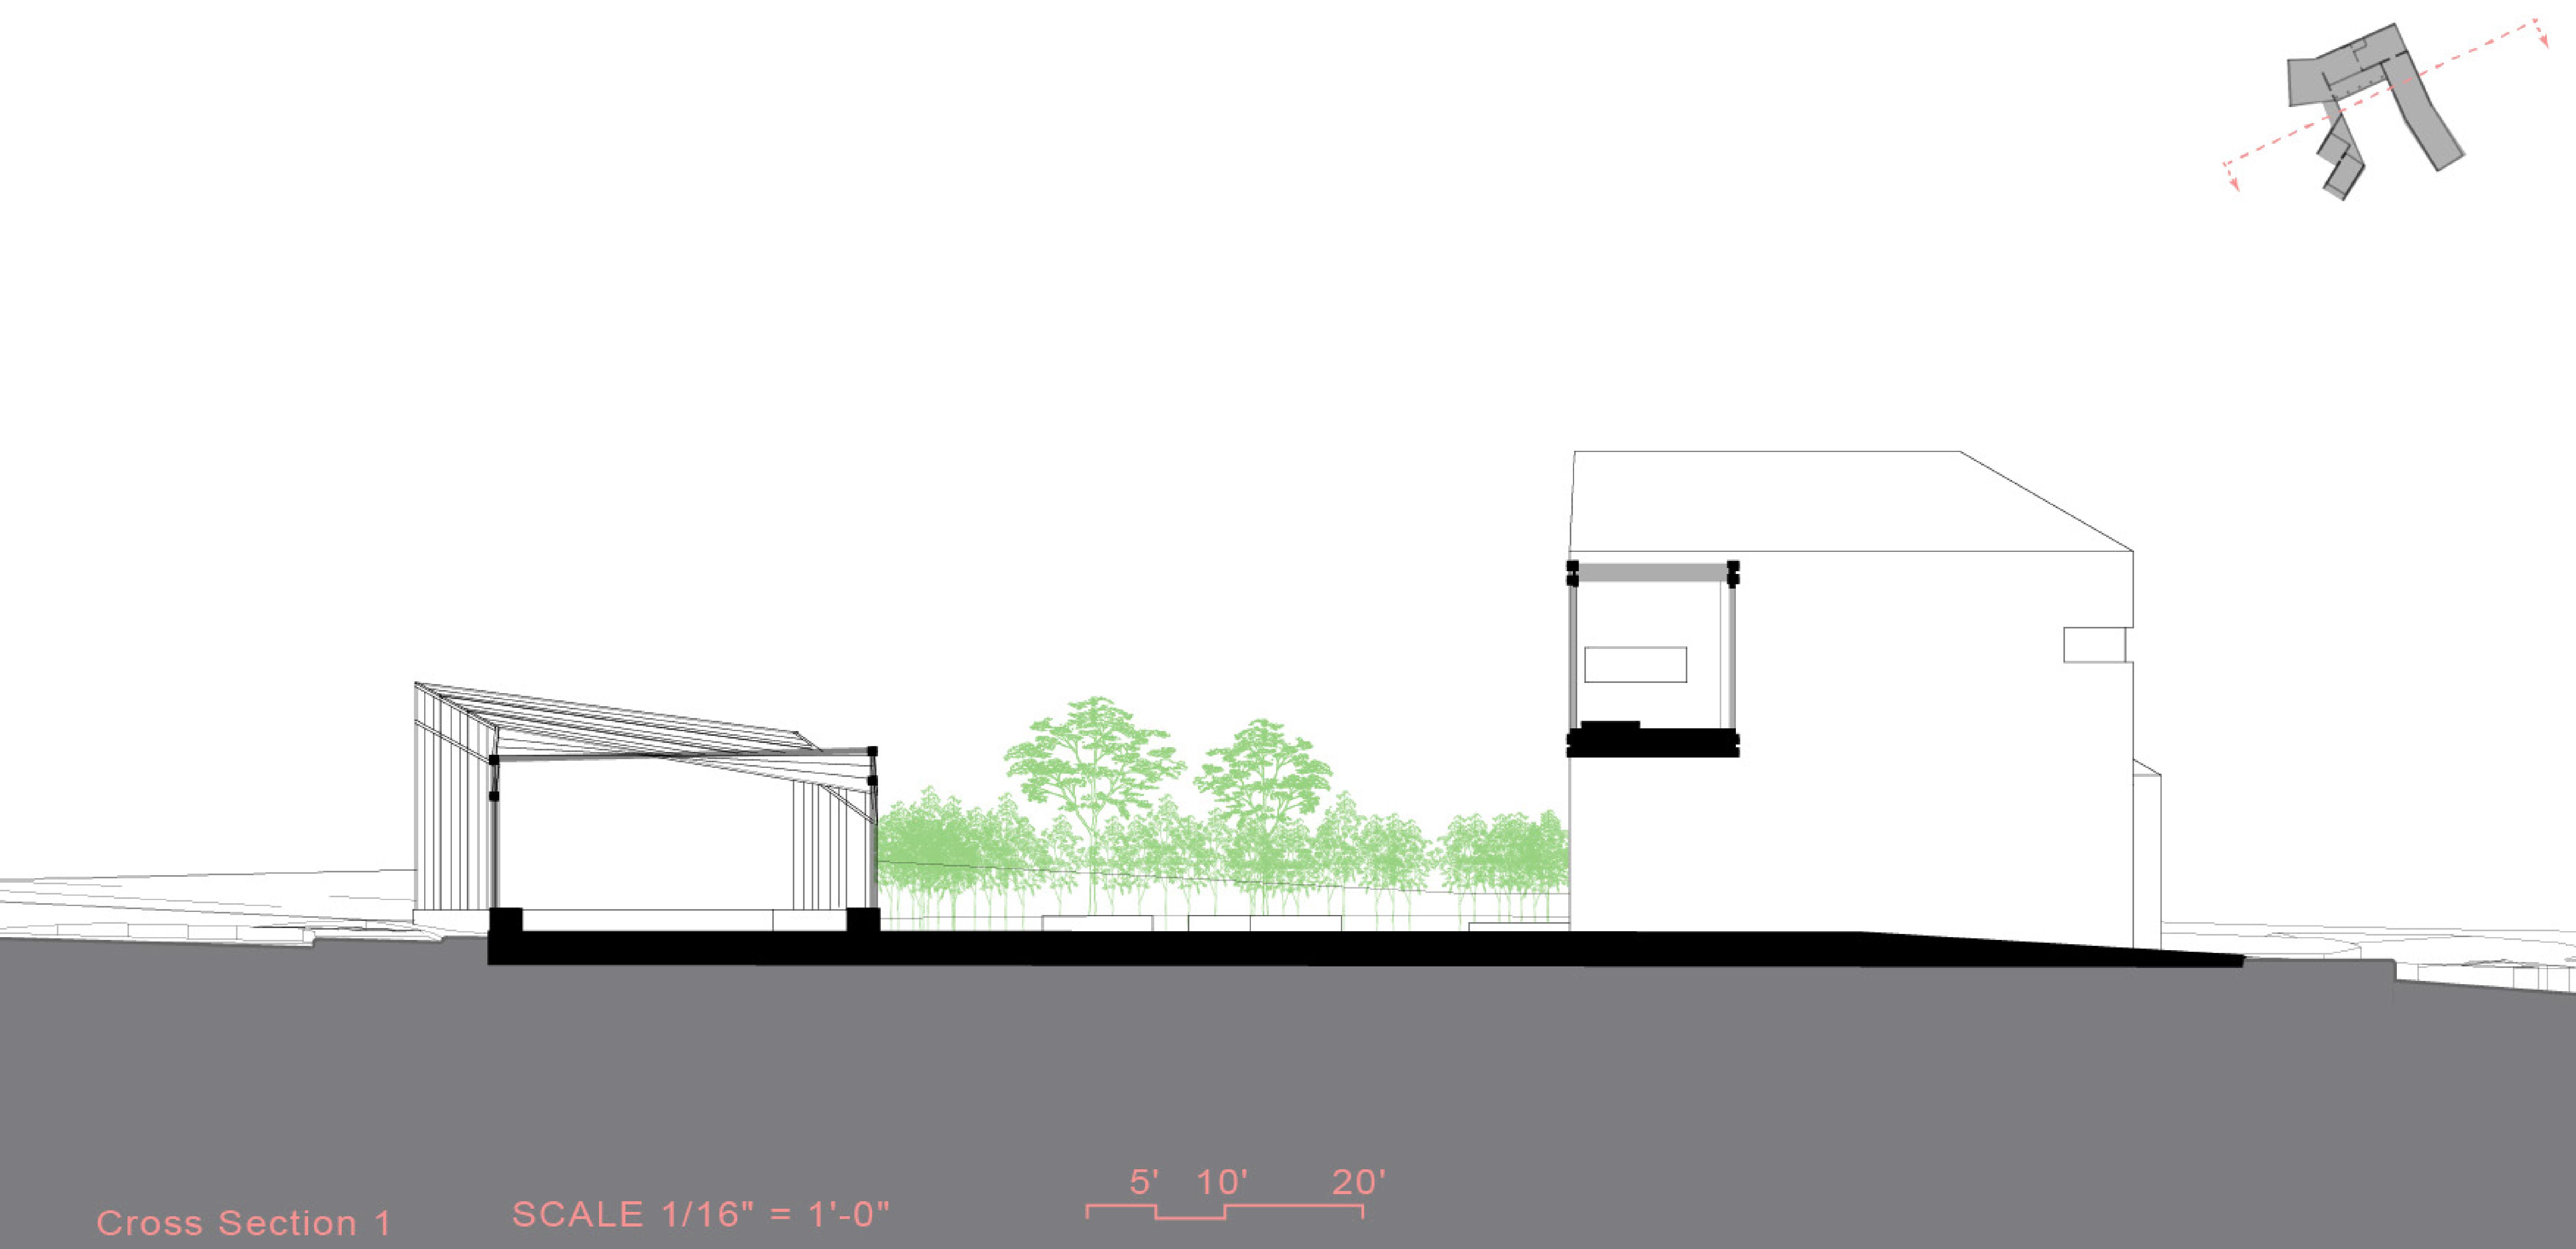

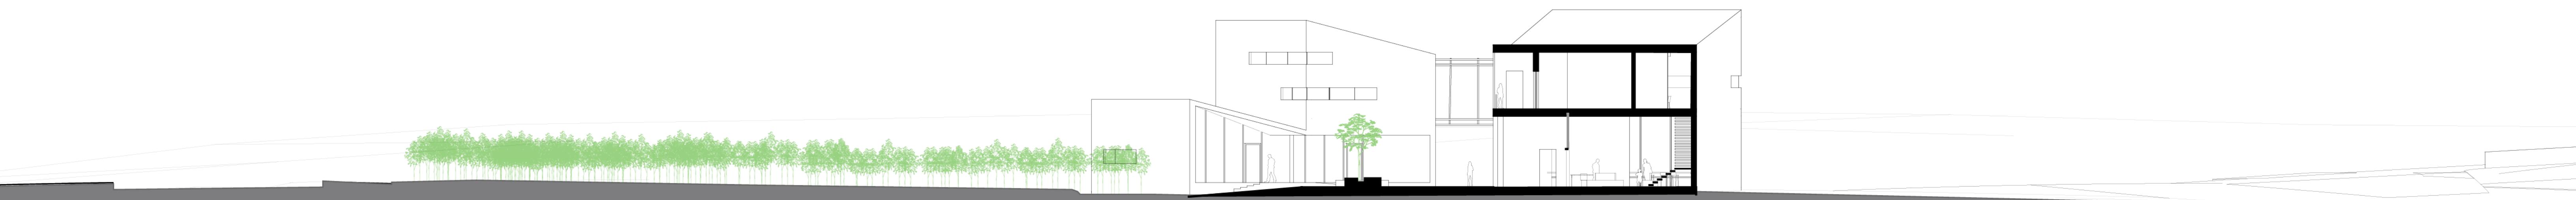





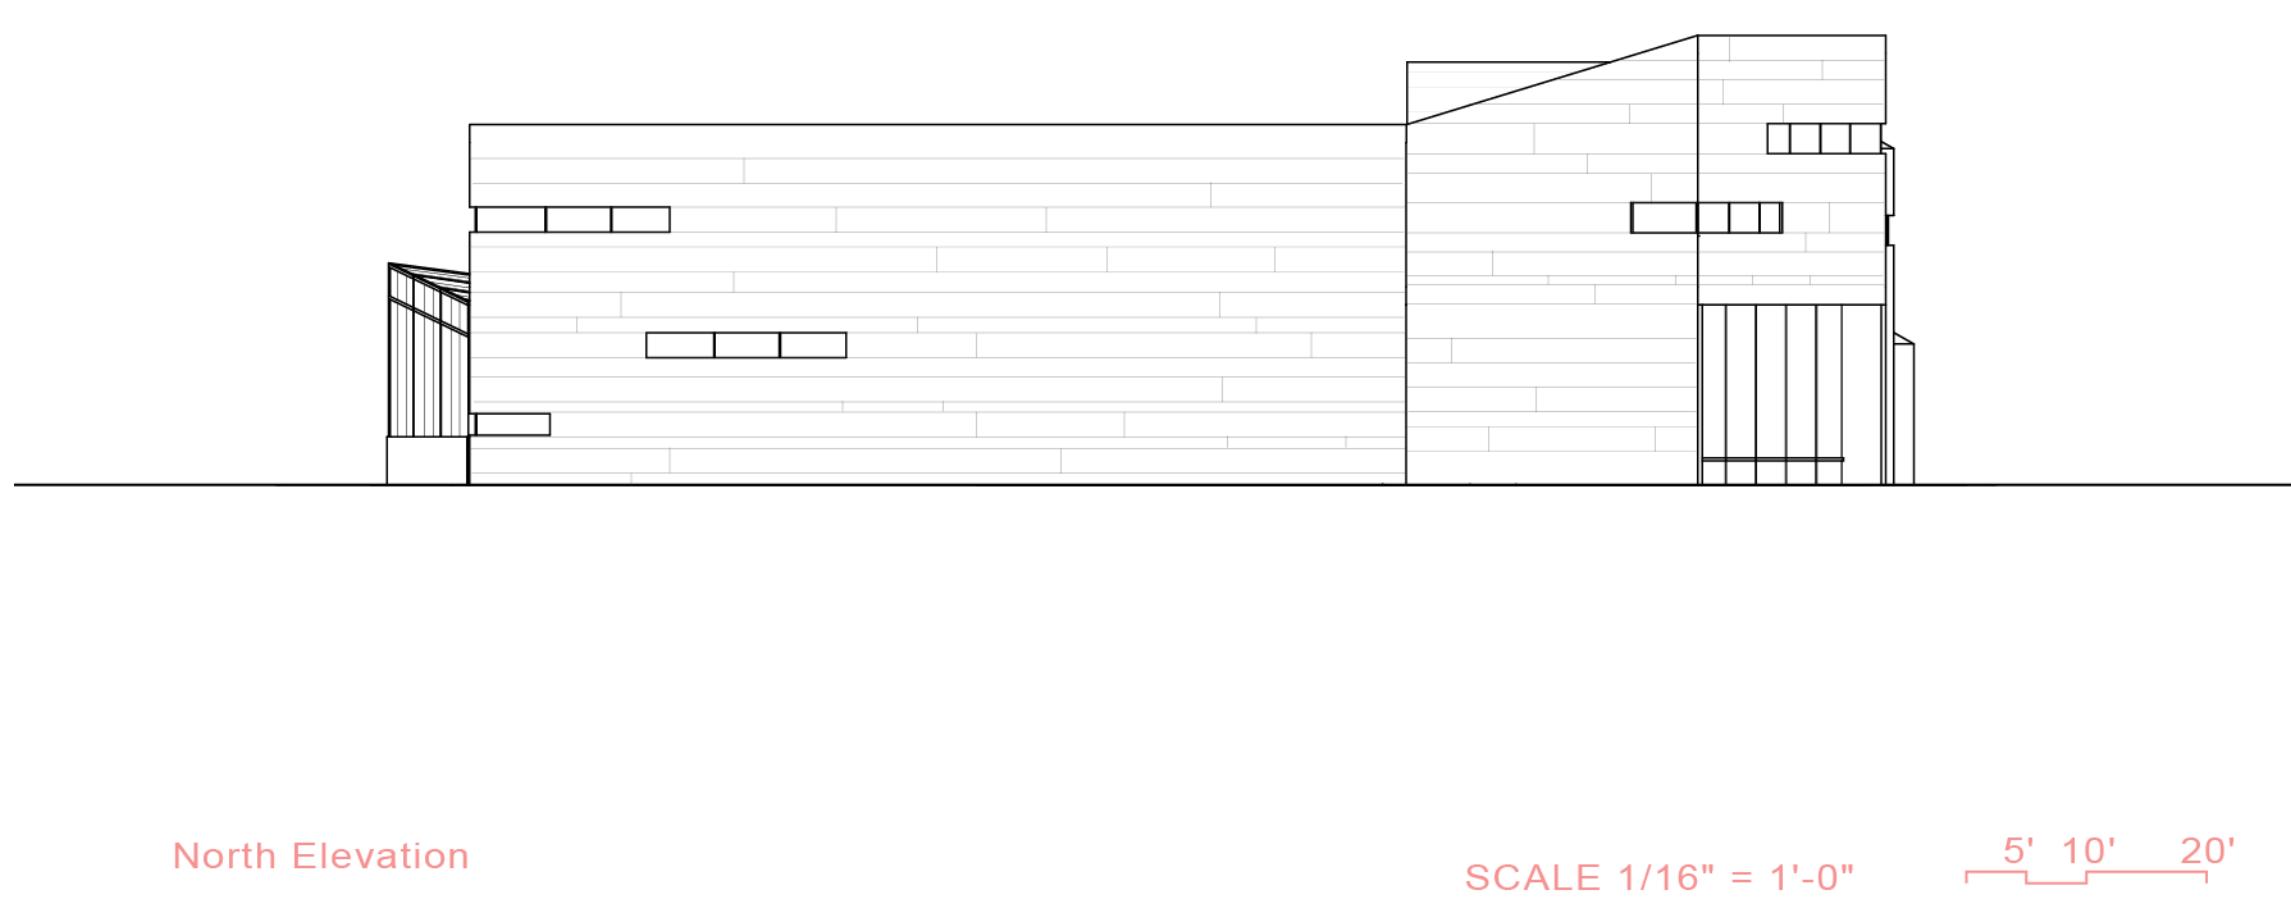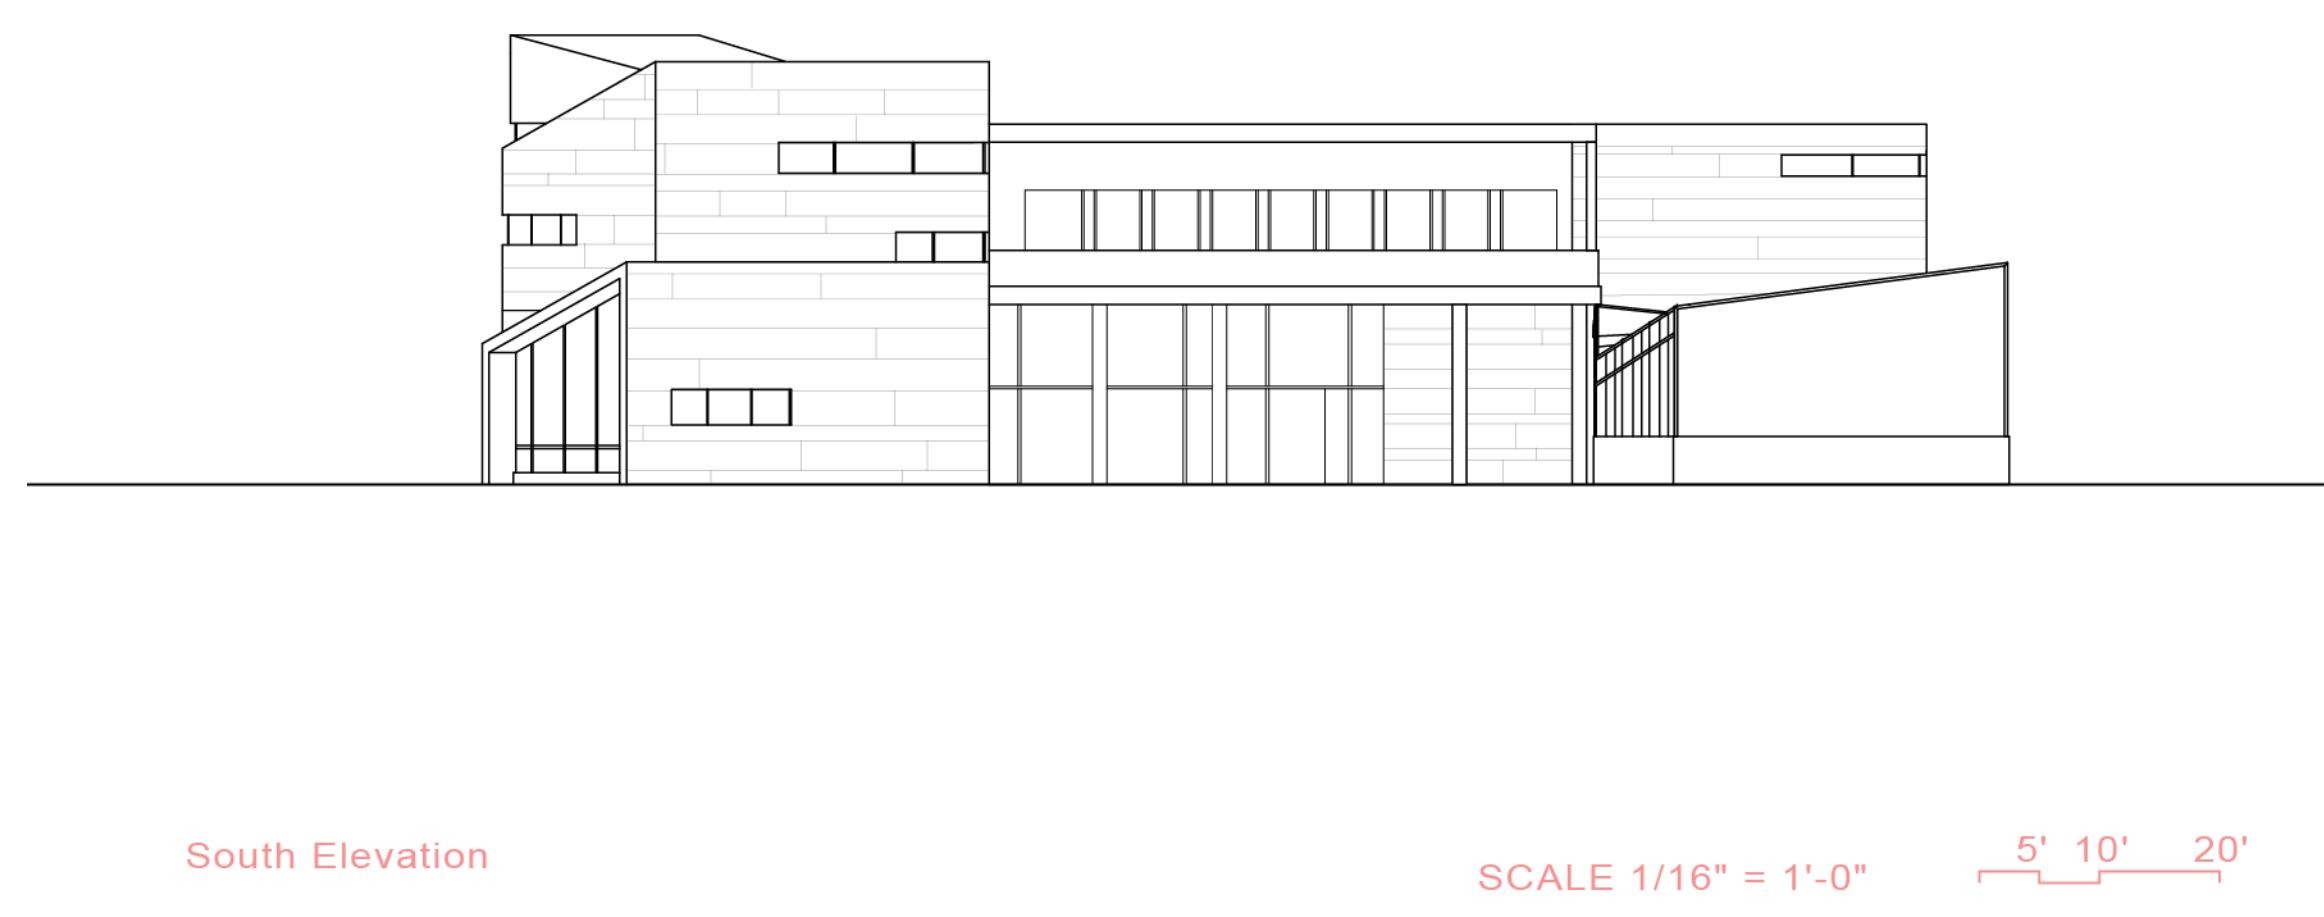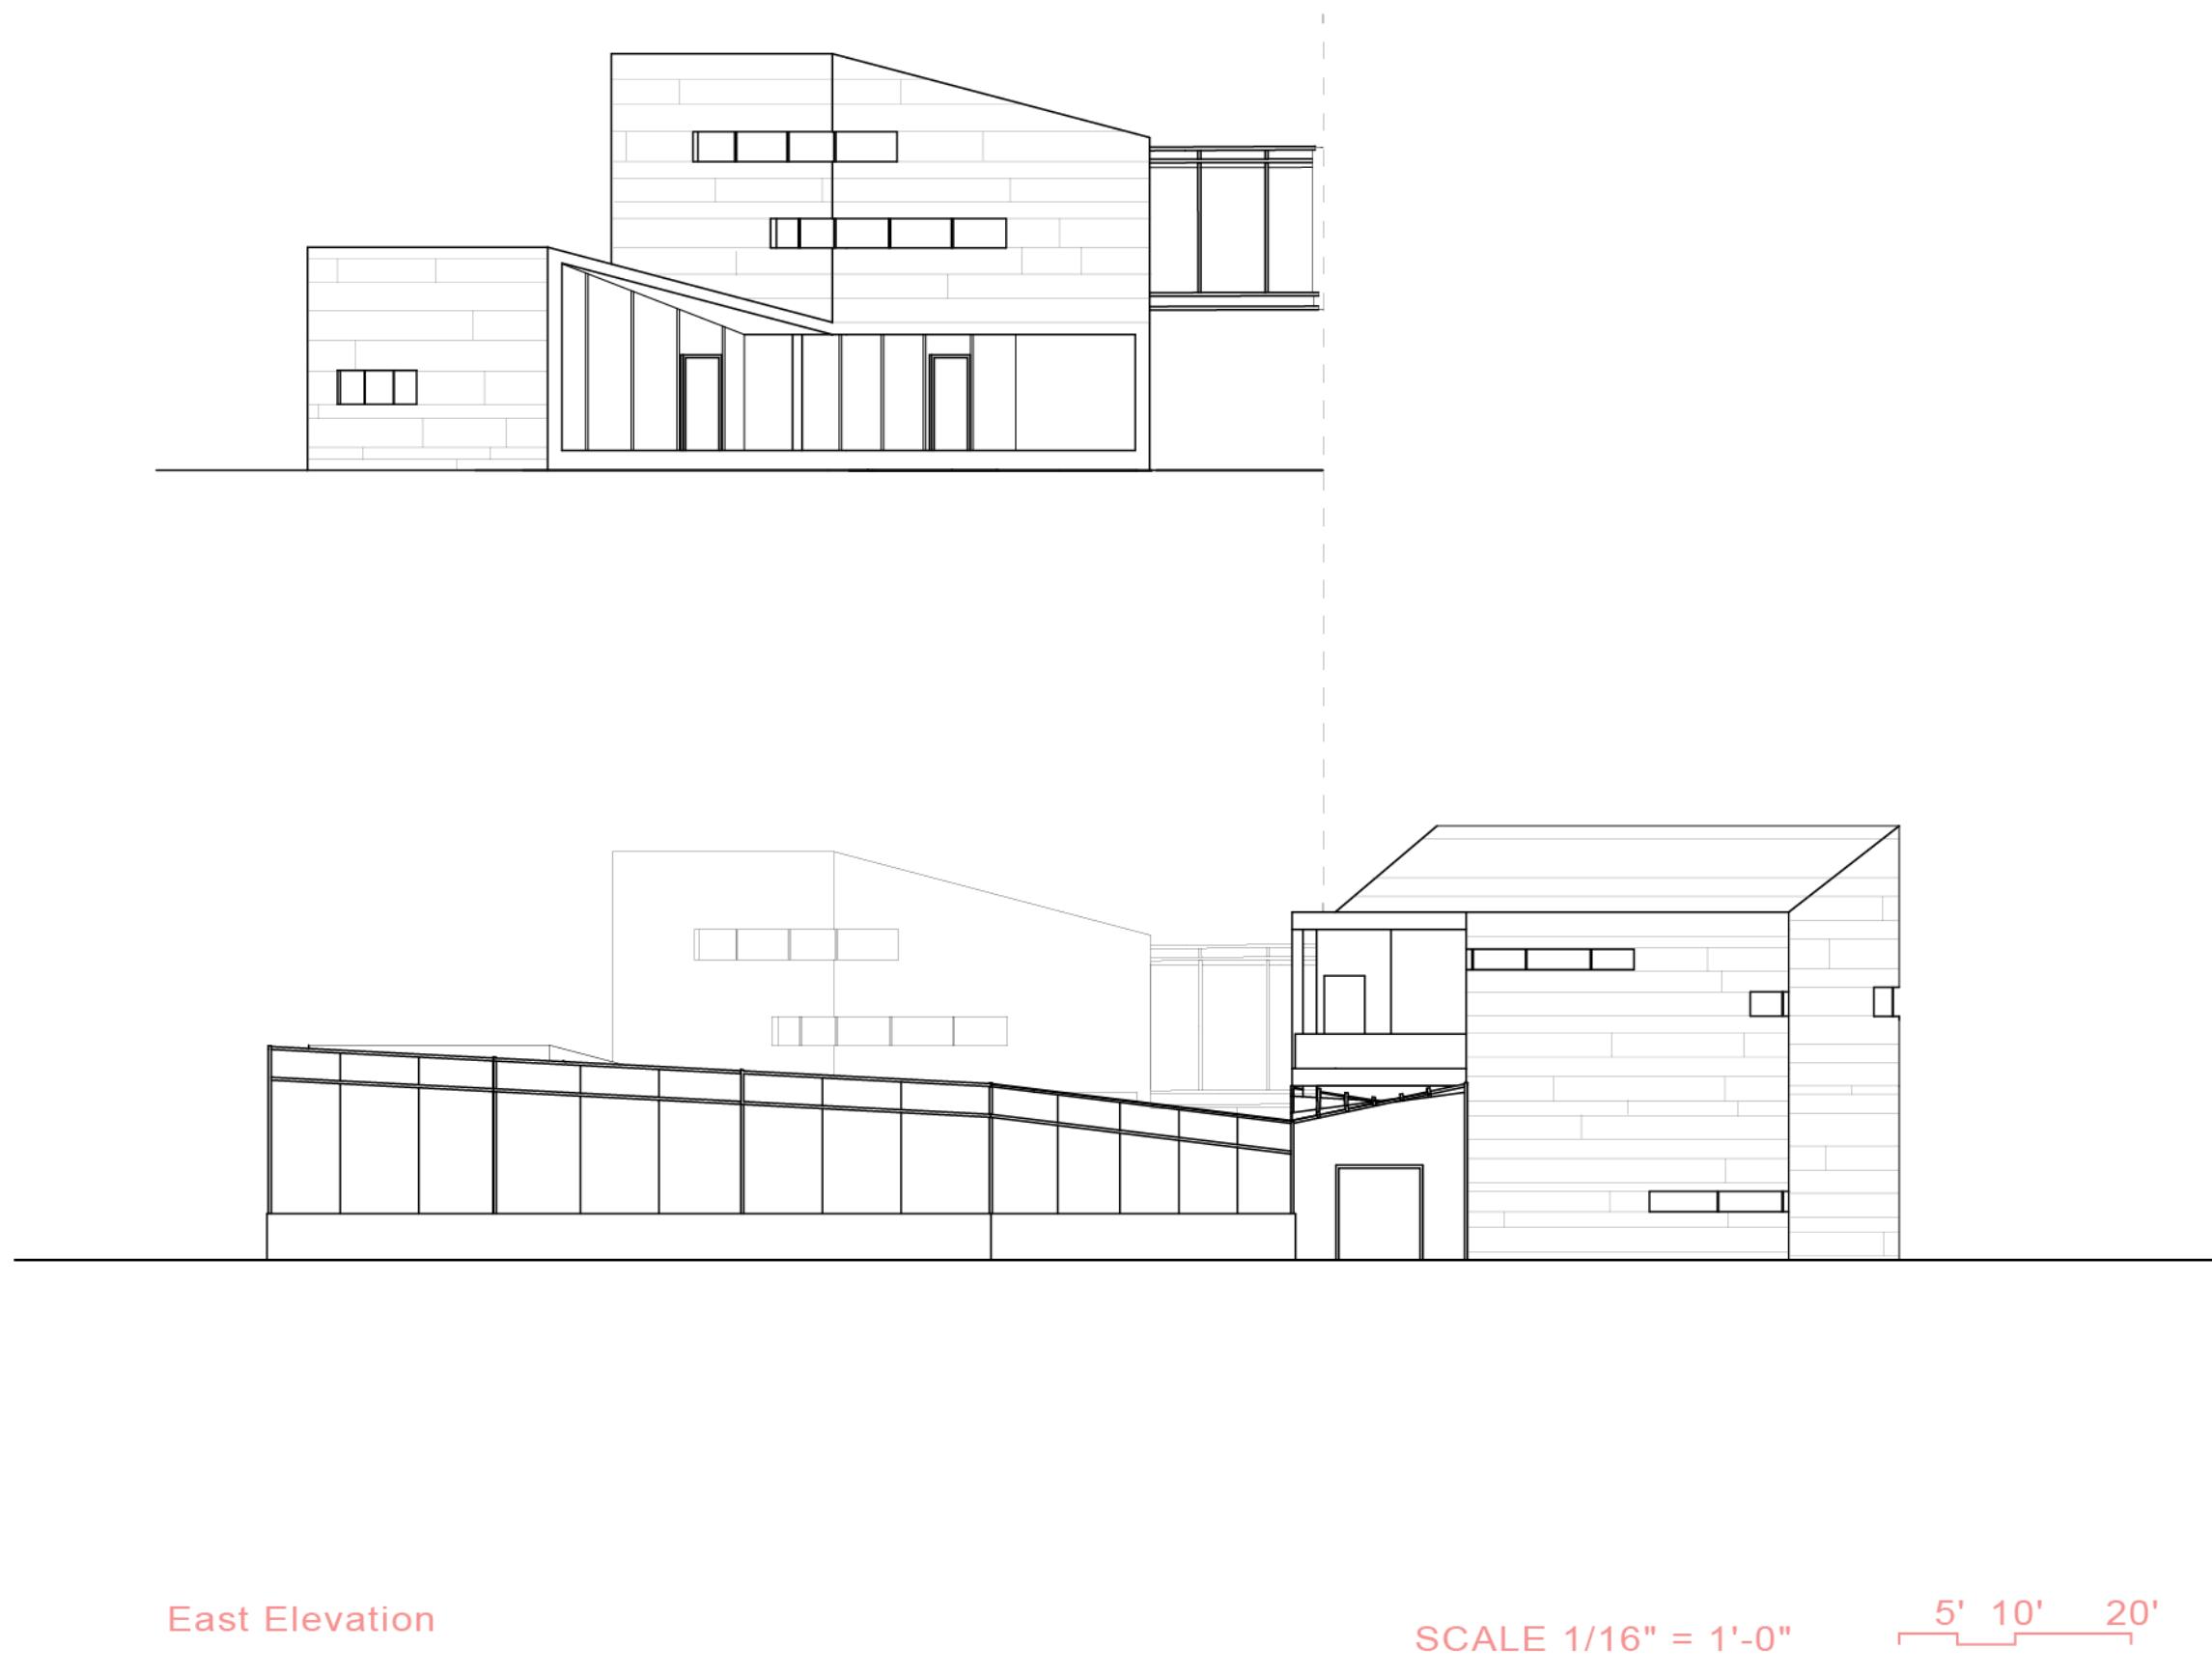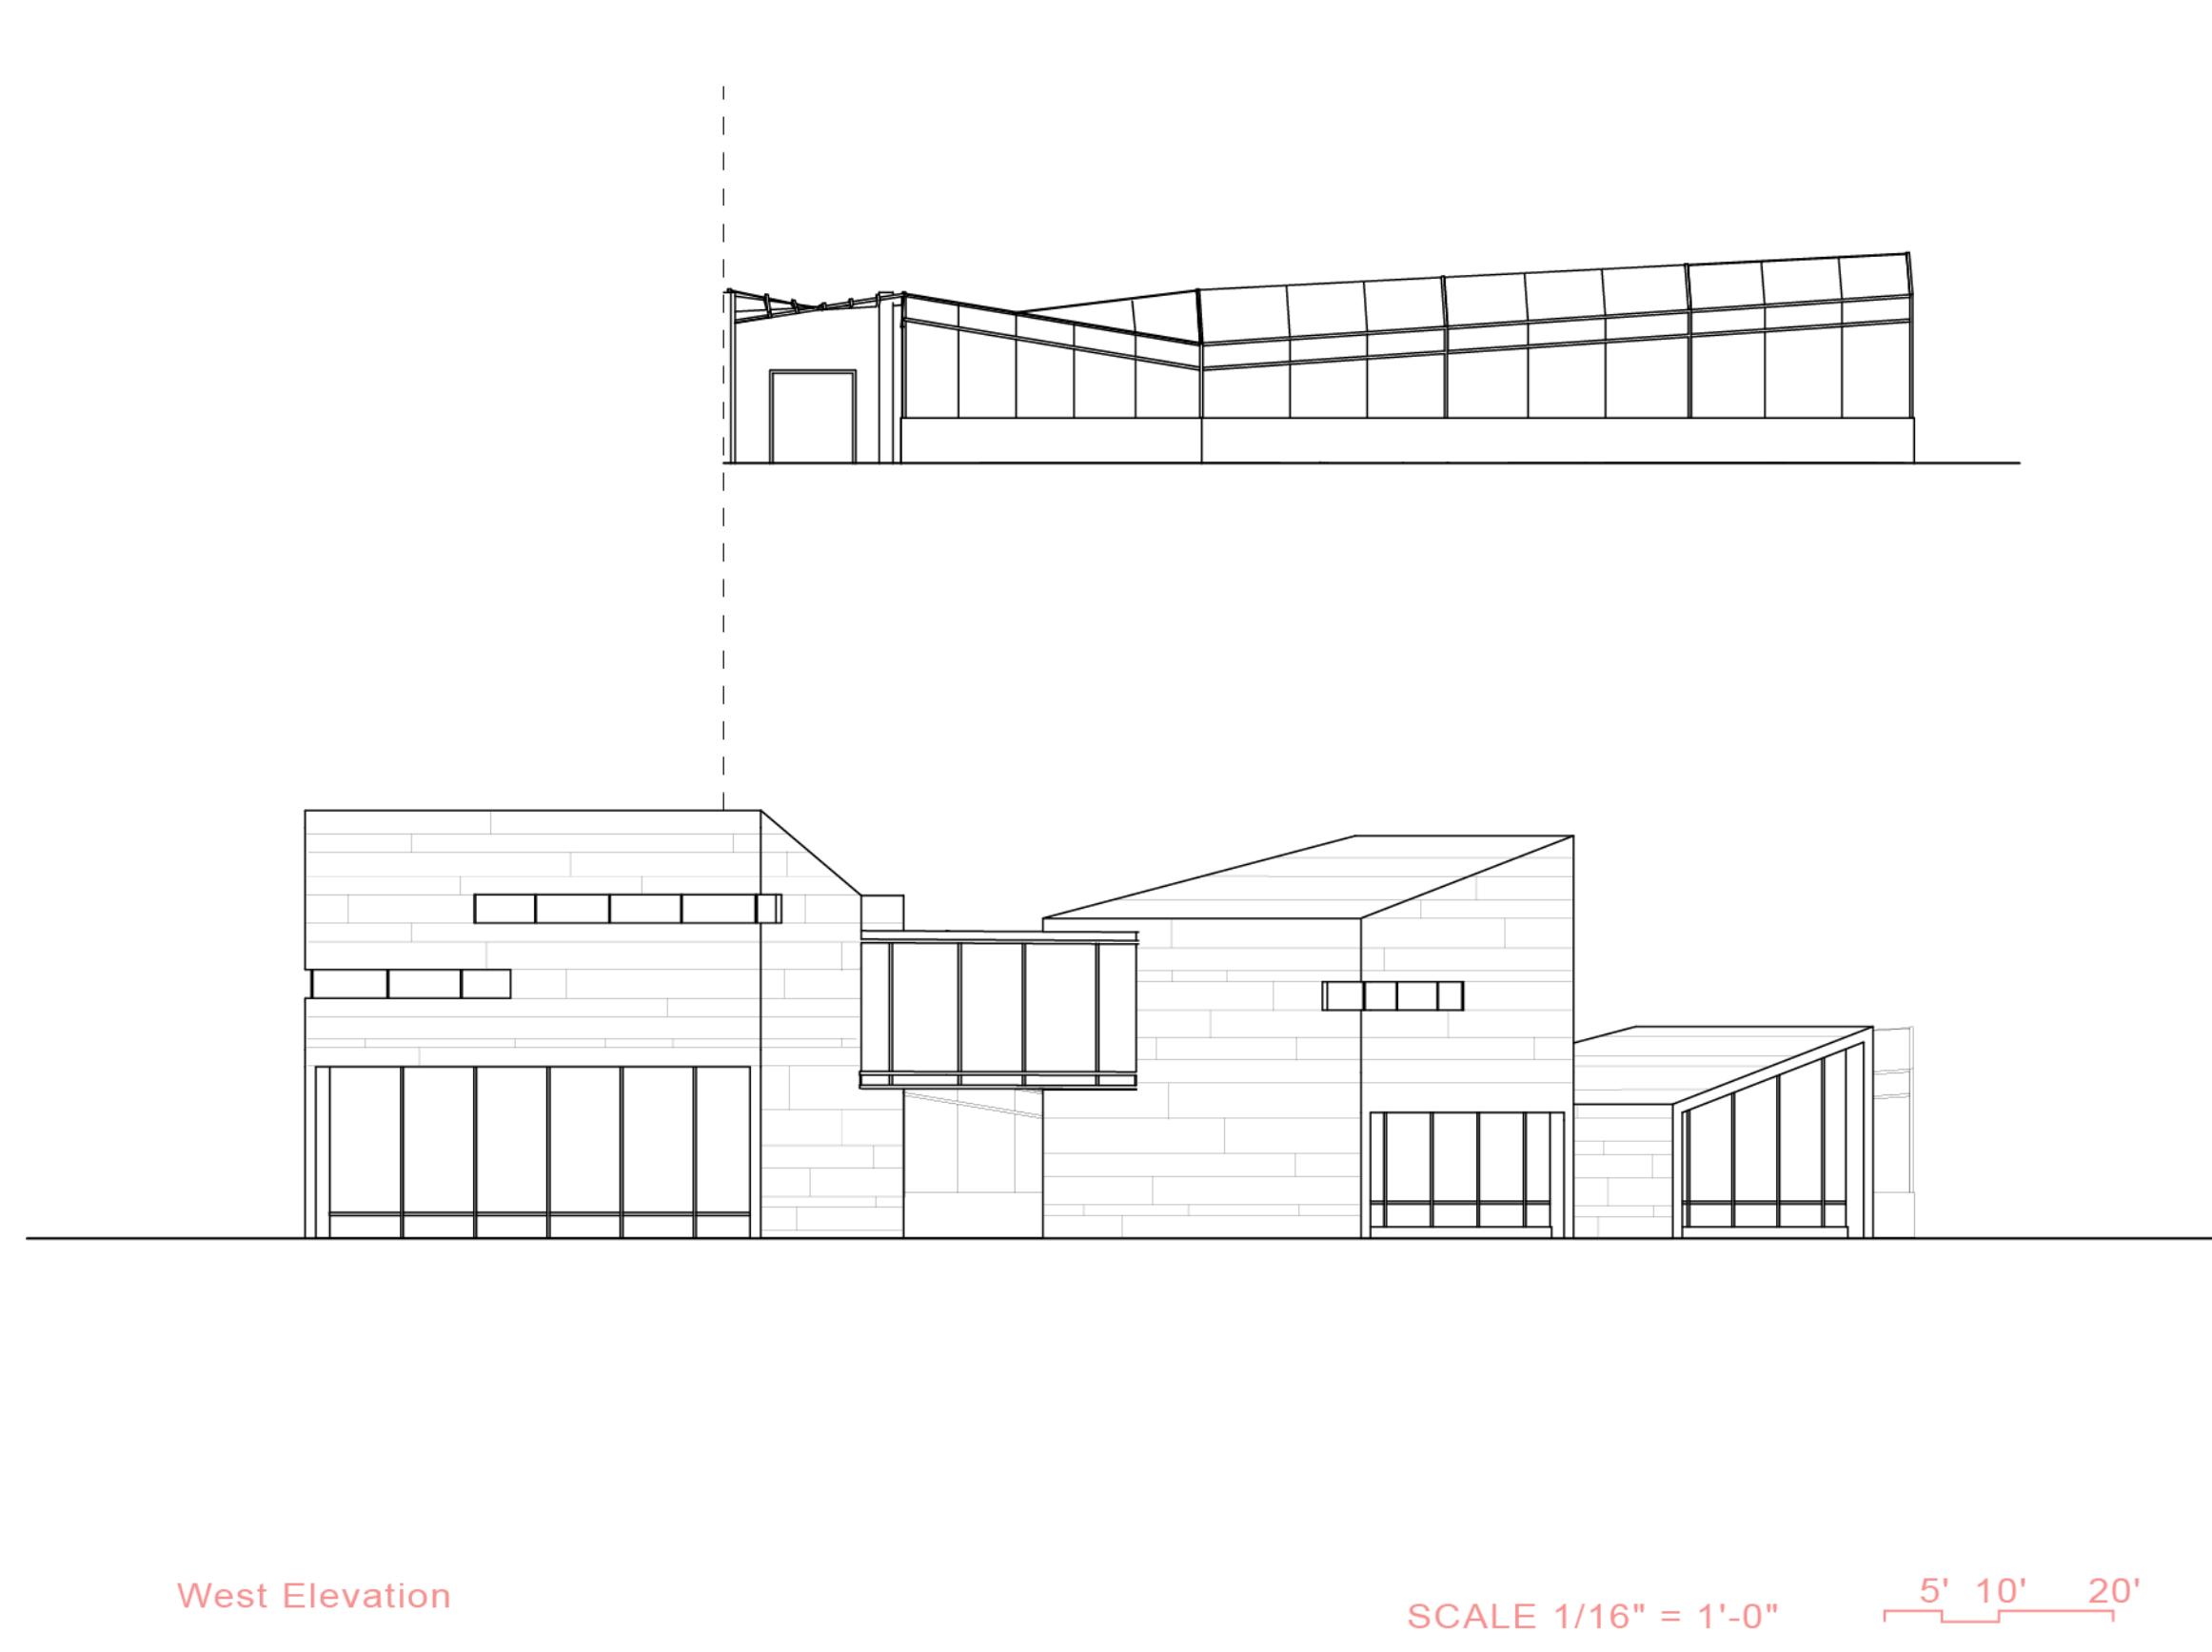





Thank you!

Lucia Tian
INTERMEDIATE ARCHITECTURAL DESIGN
Brown University